

1. GENERAL NOTES

1.1. ALL STRUCTURAL DRAWINGS SHALL BE READ IN CONJUNCTION WITH ARCHITECTURAL AND OTHER CONSULTANTS DRAWINGS AND SPECIFICATION. ANY DISCREPANCIES SHALL BE REPORTED PRIOR TO FABRICATION AND CONSTRUCTION.

1.2. ALL REFERENCED STANDARDS TO BE THE CURRENT VERSION AT THE TIME OF CONSTRUCTION.

1.3. ALL WORK TO CONFORM TO THE CURRENT NATIONAL CONSTRUCTION CODE (NCC) OF AUSTRALIA.

1.4. CHECK ALL DIMENSIONS ON SITE. DO NOT SCALE FROM DRAWINGS. DIMENSIONS ON THE STRUCTURAL DRAWINGS ARE EXCLUSIVE OF FINISHES.

1.5. THE CONTRACTOR IS RESPONSIBLE FOR THE CONSTRUCTION METHOD AND MAINTENANCE OF SAFETY DURING THE CONSTRUCTION. SHOULD ANY ELEMENT PRESENT ITSELF TO BE DIFFICULT WITH RESPECT TO CONSTRUCIBILITY OR SAFETY, THE ENGINEER IS TO BE NOTIFIED IMMEDIATELY TO ALLOW FOR DIRECTION TO BE GIVEN PRIOR TO PROCEEDING WITH WORKS.

1.6. THE STRUCTURE HAS BEEN DESIGNED TO MEET THE REQUIREMENTS OF THE RELEVANT CODE / STANDARD PROVISION FOR THE STRUCTURE IN ITS SERVICE CONDITION.
2. FOOTING NOTES

2.1. REFER TO THE GEOTECHNICAL FOR THE SPECIFIC SITE CLASSIFICATION (DEFINED IN AS2870).

2.2. ALL EARTHWORKS SHALL BE IN ACCORDANCE WITH AS3798 "GUIDELINES ON EARTHWORKS FOR COMMERCIAL AND RESIDENTIAL DEVELOPMENTS".

2.3. REFER TO GEOTECHNICAL REPORT FOR THE SPECIFIC SITE EARTHWORKS RECOMMENDATIONS.

2.4. ALL SAND SHALL BE CLEAN WELL GRADED SAND AND SHALL BE COMPACTED IN 300mm LAYERS. ALL SAND FILL SHALL BE BEAL, FREE DRAINING, WELL GRADED SAND WITH NO MORE THAN 5% PASSING A 75µm SIEVE. WHERE ENGINEER CONTROLLED FILL IS REQUIRED, THE SAND IS TO BE COMPACTED IN LAYERS OF 300mm TO ACHIEVE AT LEAST 7 PSP BLOWS FROM 150mm-450mm, 7 PSP BLOWS FROM 450mm-750mm AND 8PSP BLOWS FROM 750mm-1050mm. FOR COHESIVE/GRAVEL SITES, MINIMUM 6 BLOWS OVER 150mm USING A DYNAMIC CONE PENETROMETER (DCP) THROUGH ALL FILL OR TO 600mm IN NATURAL GROUND.

2.5. THE FOOTING DESIGN IS WITHIN PARAMETERS OF AS2870 AND CAN BE CONSIDERED A PERFORMANCE BASED DESIGN.

2.6. PREPARE SITE SUCH THAT SURFACE RUNOFF TO DRAIN AWAY FROM FOOTINGS AND FOUNDATIONS.

2.7. THE OWNER IS TO BE REFERRED TO CSIRO BUILDING TECHNOLOGY FILE 18 "FOUNDATION MAINTENANCE AND FOOTING PERFORMANCE: A HOMEOWNER'S GUIDE".

2.8. FOOTING DESIGN IS SUITABLE TO BE CONSIDERED A PHYSICAL BARRIER AGAINST INGRESS OF TERMITES.

2.9. WHERE SERVICES PIPE PASS THROUGH THE FOOTING, SPECIFIED TOTAL THICKNESS OF THE CONCRETE DEPTH IS TO BE MAINTAINED.

2.10. ENSURE NO EXISTING SERVICES OR STRUCTURES WILL BE COMPROMISED BY THE PROPOSED WORKS ON THIS LOT. IF UNSURE, CONTACT A QUALIFIED ENGINEER FOR ADVICE PRIOR TO PROCEEDING.
3. STRUCTURAL STEEL NOTES

3.1. ALL FABRICATION, ERECTION, AND TOLERANCES OF STEEL TO BE IN ACCORDANCE WITH AS4600 "COLD FORMED STEEL STRUCTURES CODE" AND AS4100 "STEEL STRUCTURES".

3.2. THE CONTRACTOR SHALL REMAIN RESPONSIBLE AT ALL TIMES FOR PROVIDING ALL NECESSARY TEMPORARY BRACING AND OTHER SUPPORTS DURING ERECTION, TO STABILISE THE PARTIALLY CONSTRUCTED BUILDING.

3.3. ALL HOLLOW SECTIONS (CHS, RHS AND SHS) SHALL COMPLY WITH AS 1163 - STRUCTURAL STEEL HOLLOW SECTIONS.

3.4. U.N.O. MINIMUM WELD FOR HOT-ROLLED SECTIONS TO BE 5mm FW. ALL WELDING SHALL BE WELD CATEGORY SP (STRUCTURAL PURPOSE) IN ACCORDANCE WITH THE S.A.A. CODE FOR WELDING OF STEEL STRUCTURES AS 1554 PART 1. FULL STRENGTH BUTT WELD (F.S.B.W.) TO BE GP WELDED CATEGORY U.N.O.

3.5. ALL BOLTS SHALL BE GRADE 4.6/S CADMIUM PLATED OR GALVANIZED UNLESS OTHERWISE NOTED.

3.6. THE CONTRACTOR SHOULD SUBMIT TO THE ENGINEERS FOR APPROVAL OF THE STEEL SHOP DRAWINGS BEFORE COMMENCING FABRICATION.

3.7. PROVIDE HOLES OR FIXING CLEATS FOR OTHER TRADES AS DIRECTED IN THE SPECIFICATION OR SHOWN ON THE ARCHITECTURAL DRAWINGS.

3.8. SEAL ALL OPEN ENDS OF HOLLOW SECTION MEMBERS. GRIND OFF ALL VISIBLE WELDS AND BRAND MARKS TO NEAT APPEARANCE WHERE SPECIFIED.

3.9. PARTICULAR ATTENTION MUST BE PAID TO THE BUCKLING STABILITY OF BEAMS AND COLUMNS PRIOR TO THE CONNECTION OF PURLINS, GIRTS, FLYBRACES AND OTHER BRACING ELEMENTS.

3.10. IT IS THE RESPONSIBILITY OF THE BUILDER TO OBTAIN PROPER TECHNICAL ADVICE WHEREVER NECESSARY TO ENSURE THE PARTIALLY COMPLETED STRUCTURE IS SAFE FROM COLLAPSE.

3.11. ALL CONCRETE ANCHORS SHALL BE INSTALLED STRICTLY IN ACCORDANCE WITH THE MANUFACTURER'S SPECIFICATIONS. THE BUILDER MUST ENSURE THE ANCHOR LENGTH IS ADEQUATE TO ENSURE CORRECT EMBEDMENT, BEARING IN MIND THE THICKNESS OF THE PART BEING FASTENED.
4. STEEL SURFACE TREATMENT

4.1. ALL STEELWORK (INCLUDING FASTENERS) SHALL COMPLY WITH WITH AS2312 AND PART 6.3.9 "CORROSION PROTECTION" OF THE ABCB HOUSING PROVISION.

4.2. HOT ROLLED STEEL INCLUDING CLEATS TO BE HOT-DIP GALVANIZED.

4.3. SITE WELDING TO BE POWER TOOL CLEANED AND PAINTED WITH TWO COATS OF ZINC SILICATE PAINT (75 MICRON MINIMUM DRY THICKNESS).

5. CONCRETE NOTES:
- 5.1. ALL CONCRETE SHALL BE IN ACCORDANCE WITH THE CONCRETE STRUCTURES CODE AS 3600.

5.2. ALL CEMENT SHALL CONFORM TO AS 3972, ALL CEMENT TO BE USED GENERAL PURPOSE CEMENT "TYPE GP". BLENDED CEMENT TYPE "GB" SHALL NOT BE USED WITHOUT THE PRIOR WRITTEN APPROVAL OF THE ENGINEER.

5.3. REFER TABLE FOR 28 DAY CYLINDER STRENGTH AND SLUMP VALUES.

5.4. REINFORCEMENT SHALL BE IN ACCORDANCE WITH THE FOLLOWING STANDARDS;

R

L

SL

N

INDICATES PLAIN REINFORCING BAR R250N TO AS/NZS 4671

INDICATES PLAIN OR DEFORMED WIRE R500L OR D500L TO AS/NZS 4671

INDICATES DEFORMED SQUARE MESH D500L TO AS/NZS 4671

INDICATES DEFORMED BARS D500N TO AS/NZS 4671
- 5.5. REINFORCEMENT SHALL BE PLACED WITH ACCURATE COVER AS PER TABLE BELOW. ALL REINFORCEMENT SHALL BE INSPECTED AND APPROVED BY THE ENGINEER PRIOR POURING CONCRETE.
- 5.6. ALL GALVANIZED ITEMS WHICH ARE CAST INTO CONCRETE ARE TO BE PASSIVATED IN A 0.2% SODIUM DICHROMATE SOLUTION OR EQUIVALENT.
- 5.7. POUR SLABS MONOLITHICALLY.
- 5.8. ALL CONCRETE SHALL BE CURED CONTINUOUSLY BY APPROVED METHODS AFTER PLACING FOR PERIODS SHOWN BELOW.

LOCATION	CONCRETE	TYPE OF CEMENT	COVER TO REINF.	MIN. CURING TIME
GROUND SLAB	N20/20/80	GB OR GP	30	3 DAYS
FOOTINGS	N20/20/100	GB OR GP	70	3 DAYS
PRE-CAST SLAB	N40/14/160 MIN	GB OR GP	30	28 DAYS

DESIGN CRITERIA

WIND DESIGN CRITERIA IN ACCORDANCE WITH AS 1170.2

WIND REGION **B2**
TERRAIN CATEGORY **2**
IMPORTANCE LEVEL **2**
ULTIMATE DESIGN WIND VELOCITY (Vu) = 57m/s
SERVICEABILITY DESIGN WIND VELOCITY (Vs) = 39m/s
Ms = 1.0, Mt = 1.0, Mzcat = 0.91, Mc = 1.05

IMPOSED ACTIONS IN ACCORDANCE WITH AS 1170.1

GENERAL AREAS 1.5kPa
BALCONIES 2.0kPa
ROOF (NON TRAFFICABLE) 0.25kPa

EARTHQUAKE DESIGN CRITERIA IN ACCORDANCE WITH AS 1170.4

PROBABILITY P = 1/500 (TABLE 3.1)
Kp = 1.0 (TABLE 3.1)
SITE HAZARD FACTOR Z ALLOWED = 0.10 (FIGURE 3.2(C))
EARTHQUAKE DESIGN CATEGORY = DOMESTIC AS PER APPENDIX A

WINDOW DESIGN CRITERIA IN ACCORDANCE WITH AS 2047 FOR HOUSING

SERVICEABILITY PRESSURE (TABLE 2.1), GENERAL - 800 Pa, CORNER WINDOWS - 1200 Pa
ULTIMATE STRENGTH PRESSURE (TABLE 2.5), GENERAL - 2000 Pa, CORNER WINDOWS - 3000 Pa
WATER PENETRATION RESISTANCE TEST PRESSURE (TABLE 2.4), NON-EXPOSED - 200 Pa,
EXPOSED - 300 Pa
CORNER WINDOWS ARE LOCATED WITHIN 1200mm OF BUILDING CORNERS.

PROVISION FOR FUTURE INSTALLATION OF ROOF-MOUNTED SOLAR PANEL

ROOF-MOUNTED SOLAR PANELS HAS BEEN CONSIDERED IN THE OVERALL STRUCTURAL ASSESSMENT. THE SELF-WEIGHT OF THE SOLAR PANEL (INCLUDING SUPPORT RAIL & FITTINGS) HAS BEEN ASSUMED TO BE 25kg/m2 (MAX)

CLIENT:	PROPERTY FRIENDS PTY LTD	Rev	Description	Date	JOB No.	25278	modularwa T: 08 64540919 F: 08 64540918 W: modularwa.com.au e: sales@modularwa.com.au Builders reg # 101630
ADDRESS:	LOT 91 BROWNLIE STREET, WAGGRAKINE WA 6530	0	Issued for construction	28/05/26	DATE:	28/05/2026 10:20:20 AM	
					DRAWN:	BT	
					CHECKED:	WI	
					REV:	SHEET	
HOUSE TYPE:	INDICATIVE - 2x1 DWELLING				SCALE:	0 1 : 100	A000
					Use figured dimensions in preference to scaled. All dimensions to be verified and checked on the job. © .		

BAL-12.5 TO AS3959-2018
CONSTRUCTION NOTES

TO COMPLY WITH SECTION 3 AND 5 OF AS3959-2018 INCLUDING BUT NOT LIMITED TO THE FOLLOWING:

FLOOR
CONCRETE SLAB ON GROUND

EXTERNAL WALLS
90mm THICK STEEL STUD SECTIONS

JOINTS
ALL JOINTS IN THE EXTERNAL SURFACE MATERIAL OF WALLS SHALL BE COVERED, SEALED, OVERLAPPED, BACKED OR BUTT-JOINTED TO PREVENT GAPS.

VENTS AND WEEPHOLES
VENTS AND WEEPHOLES IN EXTERNAL WALLS SHALL BE SCREENED WITH ALUMINIUM MESH WITH A MAXIMUM APERTURE OF 2mm.

SCREENS FOR WINDOWS & DOORS
ALUMINIUM MESH SCREEN WITH A MAX. APERTURE OF 2mm AND BE TIGHT FITTING TO THE WINDOW/DOOR FRAME. FRAME SUPPORTING MESH SHALL BE ALUMINIUM.

WINDOW / GLAZING (UNLESS NOTED OTHERWISE)
POWDER-COATED ALUMINIUM FRAMED. WHERE GLAZING IS LESS THAN 400mm FROM THE GROUND, GLAZING TO BE MIN. 4mm THICK GRADE A SAFETY GLASS. OPENABLE PORTION OF WINDOW TO BE SCREENED EXTERNALLY WITH SCREENS AS DESCRIBED ABOVE.


ROOF
METAL ROOF SHEETING AND ALL ROOF ACCESSORIES TO BE NON-COMBUSTIBLE.

ROOF / WALL AND ROOF / ROOF JUNCTION SHALL BE SEALED OR PROTECTED WITH ALUMINIUM MESH WITH MAX. APERTURE OF 2mm.

ROOF TO BE FULLY SARKED. SARKING SHALL:
• BE LOCATED ON TOP OF ROOF FRAMING, EXCEPT THAT FOIL-BACKED INSULATION MAY BE FIXED ABOVE THE ROOF BATTENS; AND
• COVER THE ENTIRE ROOF INCLUDING THE RIDGE AND HIPS; AND
• EXTEND INTO THE GUTTERS AND VALLEYS.

SHEET ROOFS SHALL HAVE ANY GAPS SEALED AT THE FASCIA OR WALL LINE, HIPS AND RIDGES BY:
• ALUMINIUM MESH WITH MAX. APERTURE OF 2mm; OR
• MINERAL WOOL; OR
• OTHER NON-COMBUSTIBLE MATERIALS; OR
• A COMBINATION OF THE ABOVE ITEMS.

ROOF PENETRATION SUCH AS ROOF VENTS
• SHALL BE FITTED WITH ALUMINIUM EMBER GUARDS WITH MAX. APERTURE OF 2mm.
• SHALL BE SEALED. THE MATERIAL USED TO SEAL THE PENETRATION SHALL BE NON-COMBUSTIBLE.

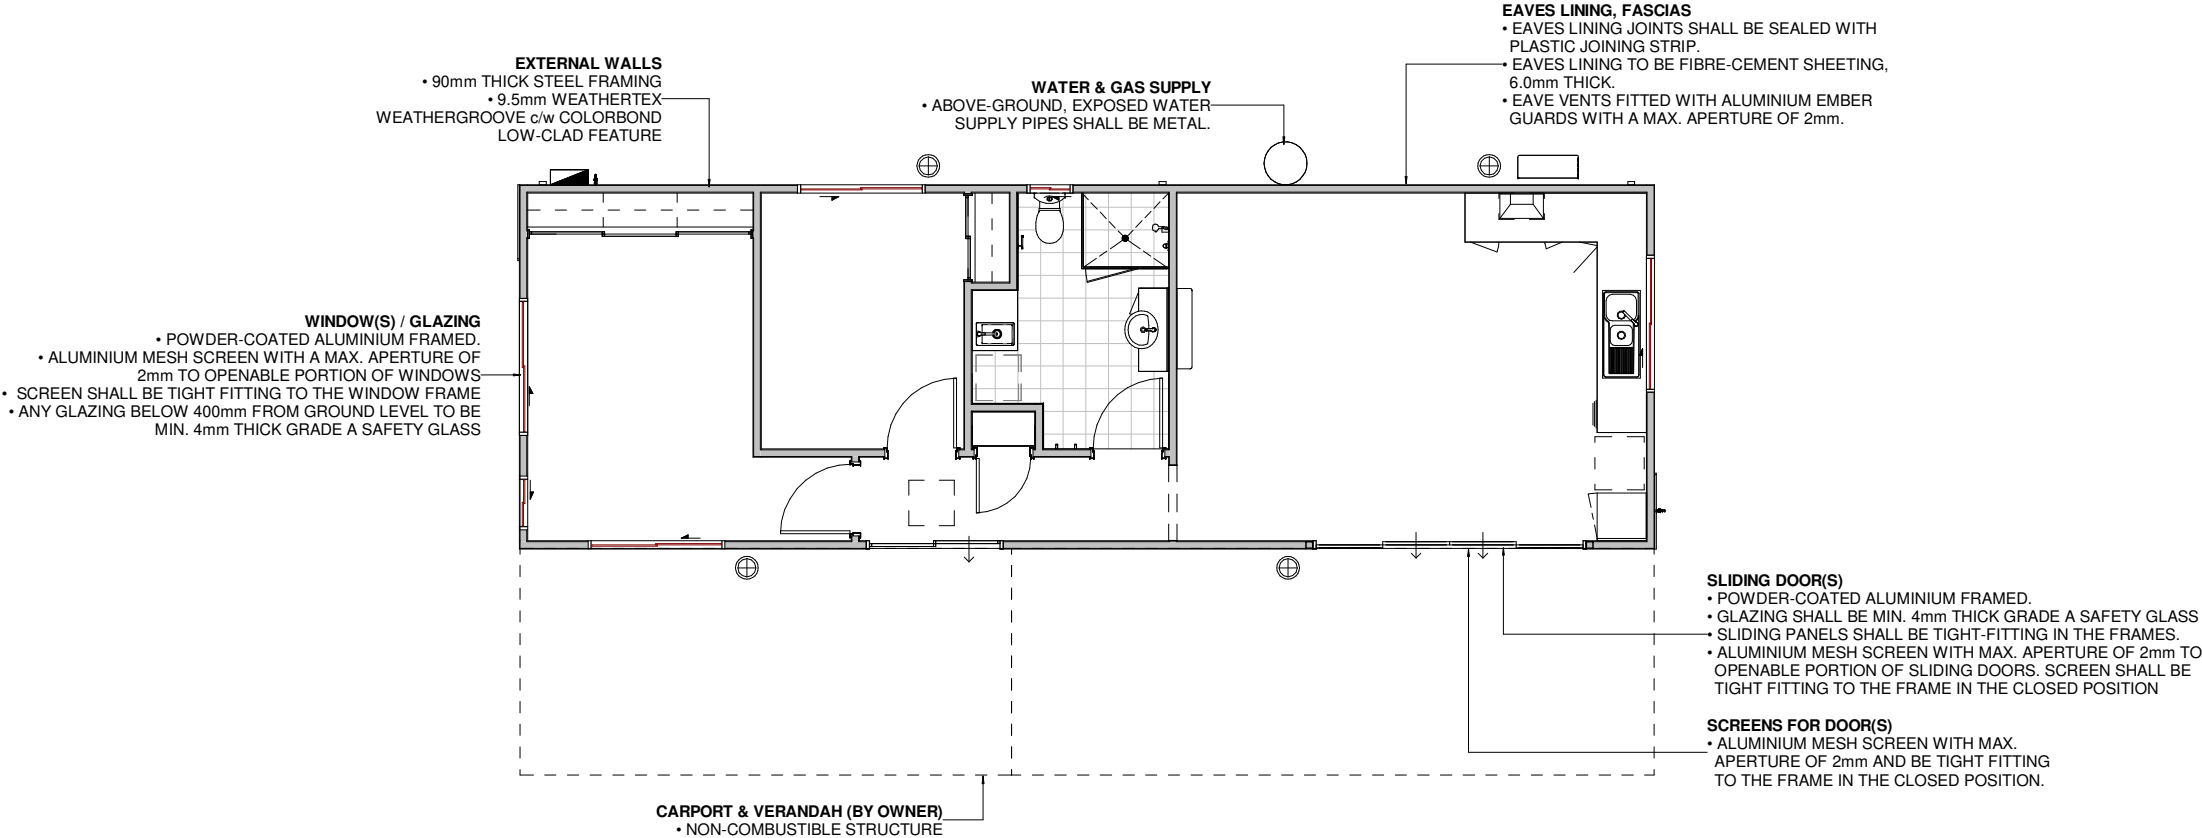

1 BUSHFIRE CONSTRUCTION PLAN
A100 1 : 100

CLIENT:	PROPERTY FRIENDS PTY LTD	<table><tr><th>Rev</th><th>Description</th><th>Date</th></tr><tr><td>0</td><td>Issued for construction</td><td>28/05/26</td></tr><tr><td> </td><td> </td><td> </td></tr><tr><td> </td><td> </td><td> </td></tr><tr><td> </td><td> </td><td> </td></tr><tr><td> </td><td> </td><td> </td></tr></table>	Rev	Description	Date	0	Issued for construction	28/05/26													JOB No.	25278	 T: 08 64540919 F: 08 64540918 W: modularwa.com.au e: sales@modularwa.com.au Builders reg # 101630
Rev	Description		Date																				
0	Issued for construction		28/05/26																				
ADDRESS:	LOT 91 BROWNLIE STREET, WAGGRAKINE WA 6530	DATE:	28/05/2026 10:20:20 AM																				
HOUSE TYPE:	INDICATIVE - 2x1 DWELLING	DRAWN:	BT																				
		CHECKED:	wi																				
		REV:	SHEET																				
		SCALE:	0 1 : 100	A100																			
		Use figured dimensions in preference to scaled. All dimensions to be verified and checked on the job. © .																					

F.F.L - FINISHED FLOOR LEVEL
F.B.L - FINISHED BACKFILL LEVEL
F.C.L - FINISHED CUT/COMPACT LEVEL
N.G.L - NATURAL GROUND LEVEL




- SITE NOTES:**
1. ALL BOUNDARIES, DIMENSIONS, SETBACKS AND LOCATION OF EXISTING RETAINING TO BE CONFIRMED ON RECEIPT OF SURVEY.
 2. FFL TO BE CONFIRMED ON RECIEPT OF SURVEY.
 3. SITE SERVICES AND LOCATIONS TO BE CONFIRMED ON RECEIPT OF SURVEY.
 4. NO VERGE INFRASTRUCTURE IS PROPOSED ADJACENT TO THIS LOT. THE ONLY PERMANENT SUBDIVISION INFRASTRUCTURE IN THE VICINITY IS THE STORMWATER CULVERT AT THE BROWNIE STREET / ULLA STREET INTERSECTION — REFER MONTGOMERY ENGINEERING CONSULTANTS DRAWING C212460-R-050 REV 4.

SP
A101
1 : 250
SITE PLAN

ROAD RESERVE

ULLA STREET

ROAD RESERVE

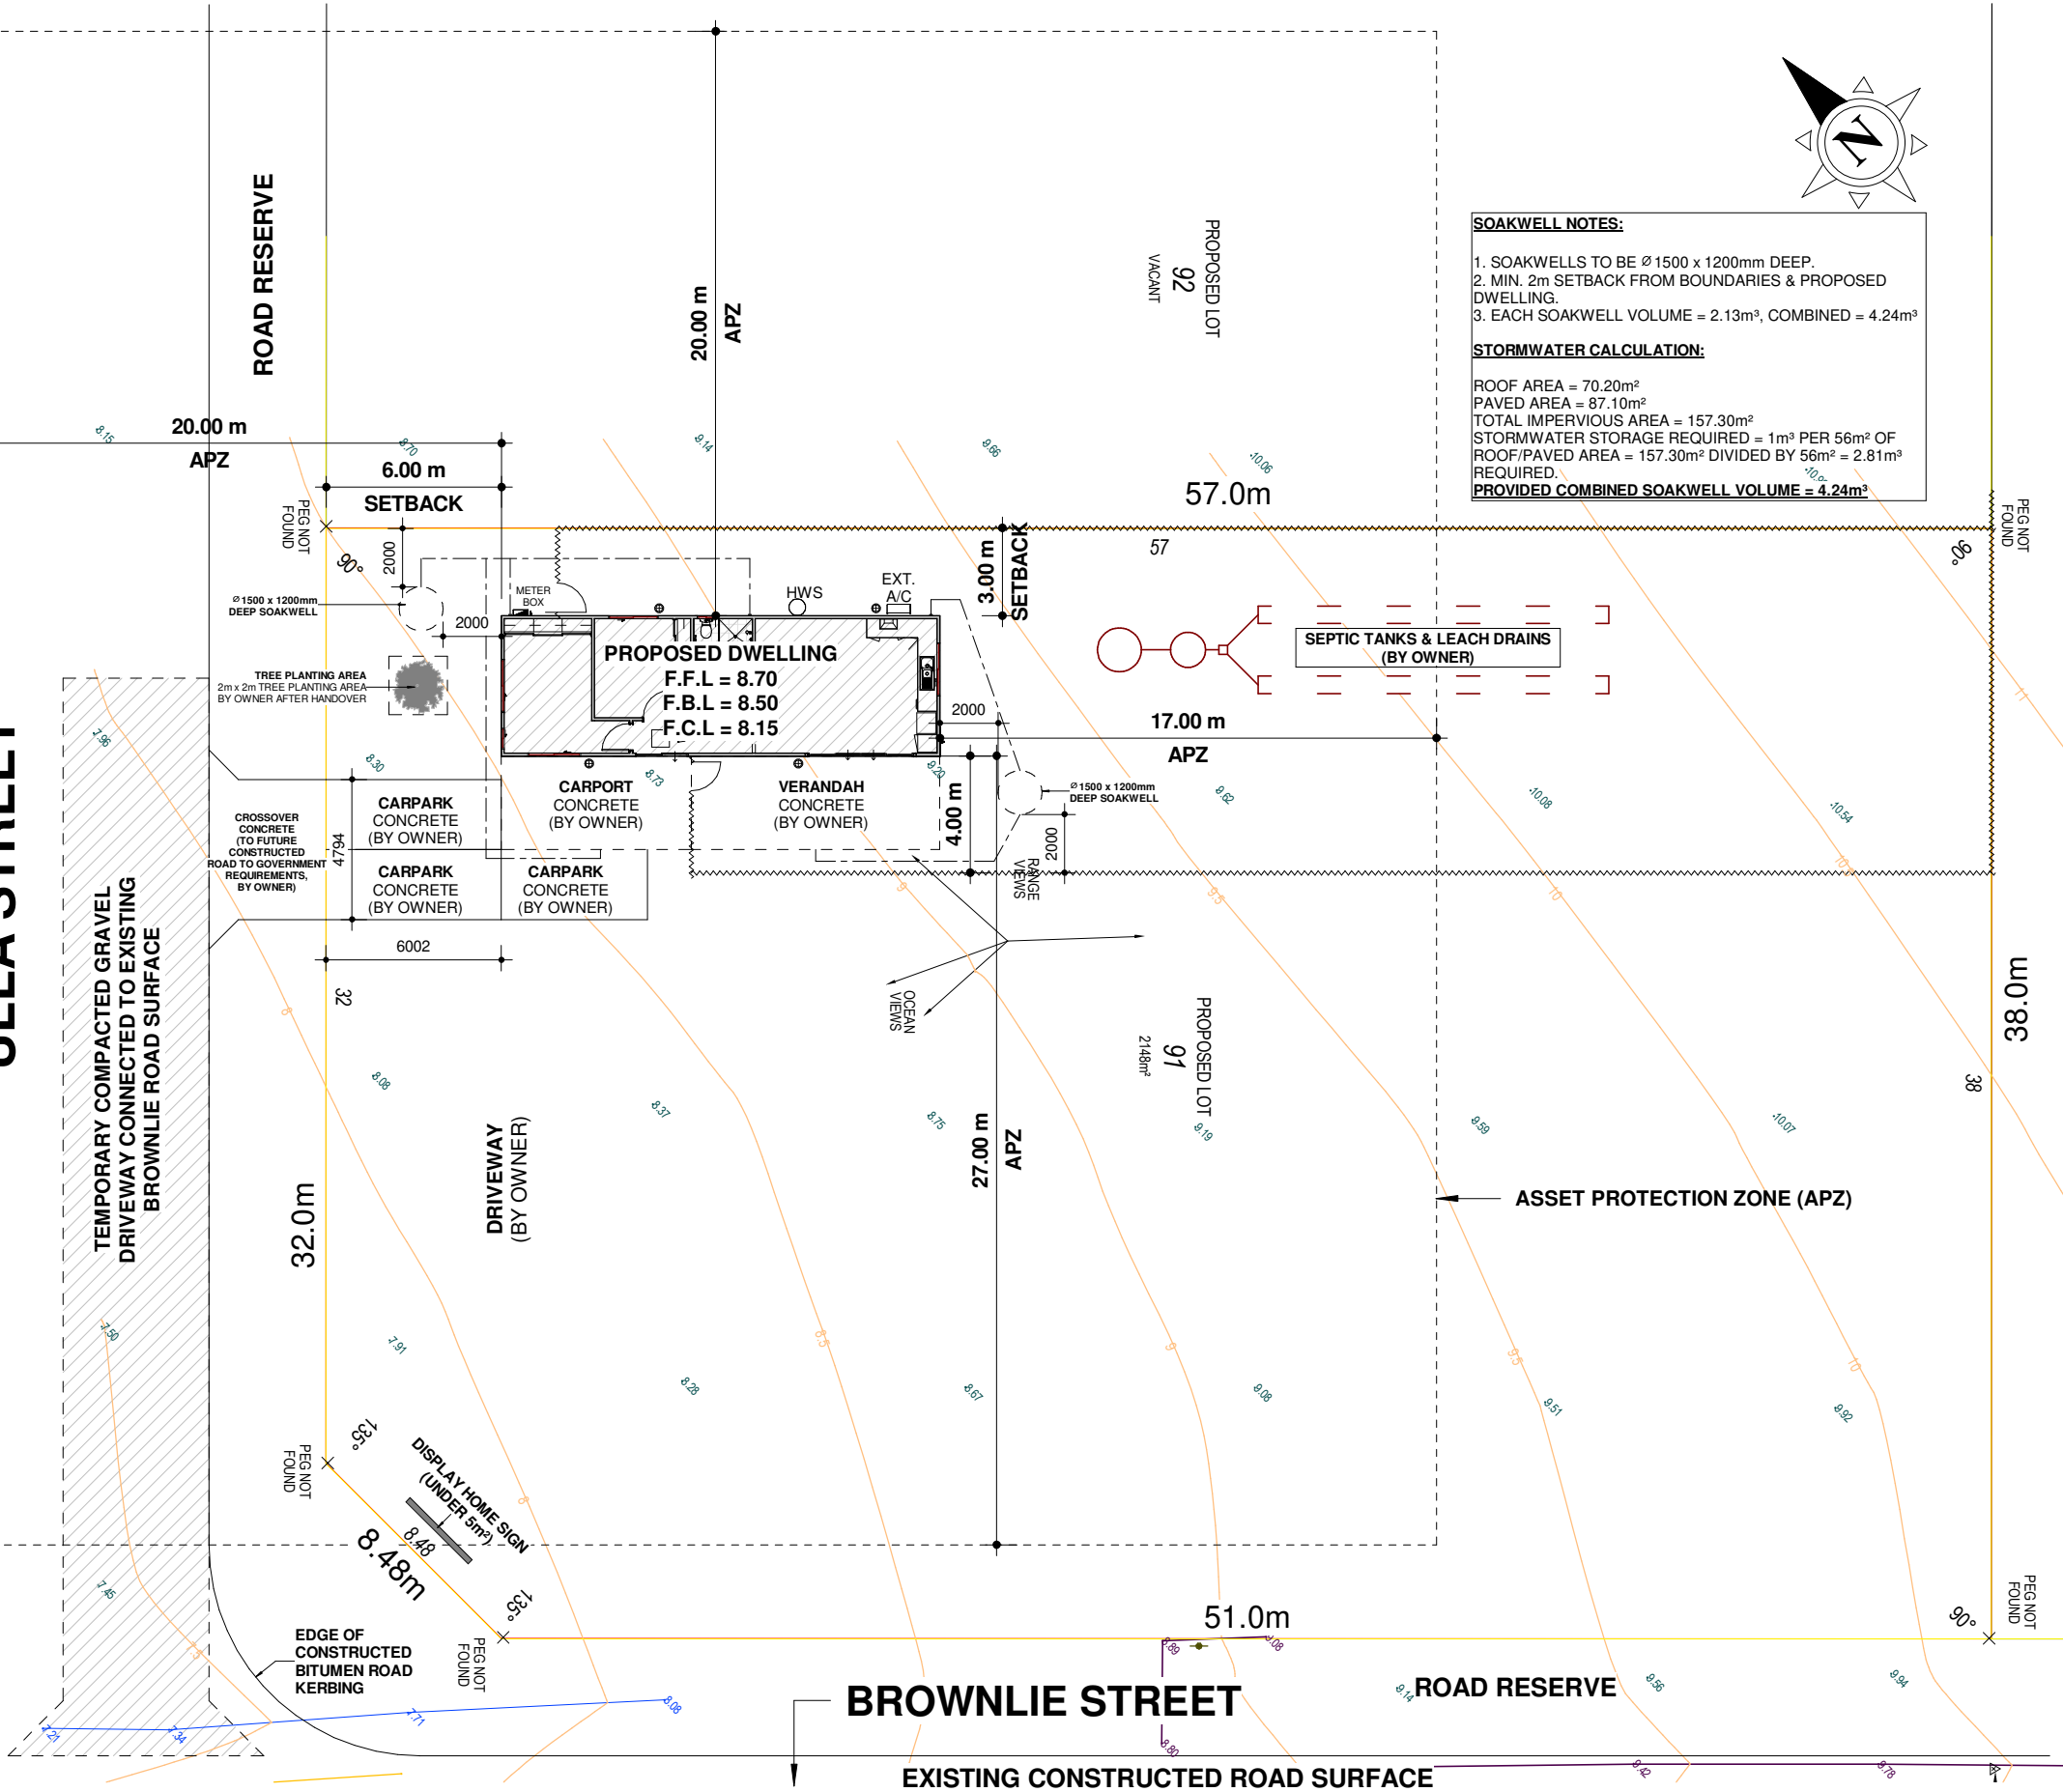

SOAKWELL NOTES:

1. SOAKWELLS TO BE Ø 1500 x 1200mm DEEP.
2. MIN. 2m SETBACK FROM BOUNDARIES & PROPOSED DWELLING.
3. EACH SOAKWELL VOLUME = 2.13m³, COMBINED = 4.24m³

STORMWATER CALCULATION:

ROOF AREA = 70.20m²
PAVED AREA = 87.10m²
TOTAL IMPERVIOUS AREA = 157.30m²
STORMWATER STORAGE REQUIRED = 1m³ PER 56m² OF ROOF/PAVED AREA = 157.30m² DIVIDED BY 56m² = 2.81m³ REQUIRED.
PROVIDED COMBINED SOAKWELL VOLUME = 4.24m³

CLIENT: **PROPERTY FRIENDS PTY LTD**

ADDRESS: **LOT 91 BROWNIE STREET,
WAGGRAKINE WA 6530**

HOUSE TYPE: **INDICATIVE - 2x1 DWELLING**

Rev	Description	Date
0	Issued for construction	28/05/26

JOB No. **25278**

DATE: 28/05/2026 10:20:20 AM

DRAWN: **BT**

CHECKED: **WI**

REV: **0**

SCALE: **A101**

As indicated

modularwa

T: 08 64540919 F: 08 64540918
W: modularwa.com.au
e: sales@modularwa.com.au
Builders reg # 101630

Use figured dimensions in preference to scaled.
All dimensions to be verified and checked on the job. ©

GENERAL NOTES:

1. DO NOT SCALE FROM THIS DRAWING. ALL CONTRACTORS TO CHECK DIMENSIONS AND NOTES PRIOR TO COMMENCEMENT OF ANY WORKS AND ANY DISCREPANCIES TO BE NOTIFIED TO THE SITE SUPERVISOR WITHOUT DELAY.
2. DIMENSIONS SHOWN ON THIS PLAN ARE TO STEEL FRAME AND DOES NOT INCLUDE EXTERNAL CLADDING OR INTERNAL LINING WIDTH.

CLIENT NOTE:

1. THIS PLAN IS TO BE READ IN CONJUNCTION WITH MODULAR WA ADDENDA AND ENGINEERED CERTIFIED DRAWINGS.

2. OWNER TO SUPPLY & INSTALL PORTABLE HOT PLATE. NO ALLOWANCE FOR BUILDER SUPPLIED HOT PLATE.

CARPENTERS NOTE:

SILICONE BEAD REQUIRED AT BASE OF WALL FRAMES TO ALL TILED WET AREAS

INTERNAL OPENINGS:

DHO: FLUSHED DOOR HEIGHT OPENING 2080mm A.F.L
FHO: FULL HEIGHT OPENING

DOORS & WINDOWS

1. WINDOW HEAD HEIGHT TO BE 2143mm A.F.L UNLESS NOTED OTHERWISE.
2. INSTALL SILL SUPPORT ANGLE TO ALL ALUMINIUM EXTERNAL SLIDING DOORS. REFER TO DETAIL.
3. ALL WINDOW & SLIDING DOOR FLYMESH TO BE ALUMINIUM TYPE.
4. NON TRANSPARENT WINDOW BLINDS BY OWNER FOR ENERGY COMPLIANCE.
5. ALL WINDOWS AND EXTERNAL SLIDING DOORS TO BE CYCLONIC RATED TO SUIT REGION B2.



ABBREVIATION LEGEND

HP	HOT PLATE
RH	RANGEHOOD
UBO	UNDERBENCH OVEN
OHC	OVERHEAD CUPBOARD
DR	DRAWER
FR/FZ REC	FRIDGE / FREEZER RECESS
DW REC	DISHWASHER RECESS
TR	TROUGH
WM REC	WASHING MACHINE RECESS
TRH	TOILET ROLL HOLDER
DTR	DOUBLE TOWEL RAIL
TRG	TOWEL RING
SR	SHOWER RAIL / ROSE
CAP	CEILING ACCESS PANEL
BRM	BROOM
V	VANITY
B	BASIN
OBS	OBSCURE
TF	TIMBER FRAME
AF	ALUMINIUM FRAME
SD	SLIDING DOOR
D	DOOR
W	WINDOW
AW	AWNING WINDOW
FW	FIXED WINDOW
COL	COLUMN
H/H	HEAD HEIGHT
RWP	RAIN WATER PIPE
SV	SUB-FLOOR VENT
LOH	LIFT OFF HINGES
Ⓟ	PRIVACY LATCH

BUSHFIRE ATTACK
LEVEL (BAL): 12.5

WIND CLASSIFICATION:
REGION "B2"

SOIL CLASSIFICATION: "TBC"

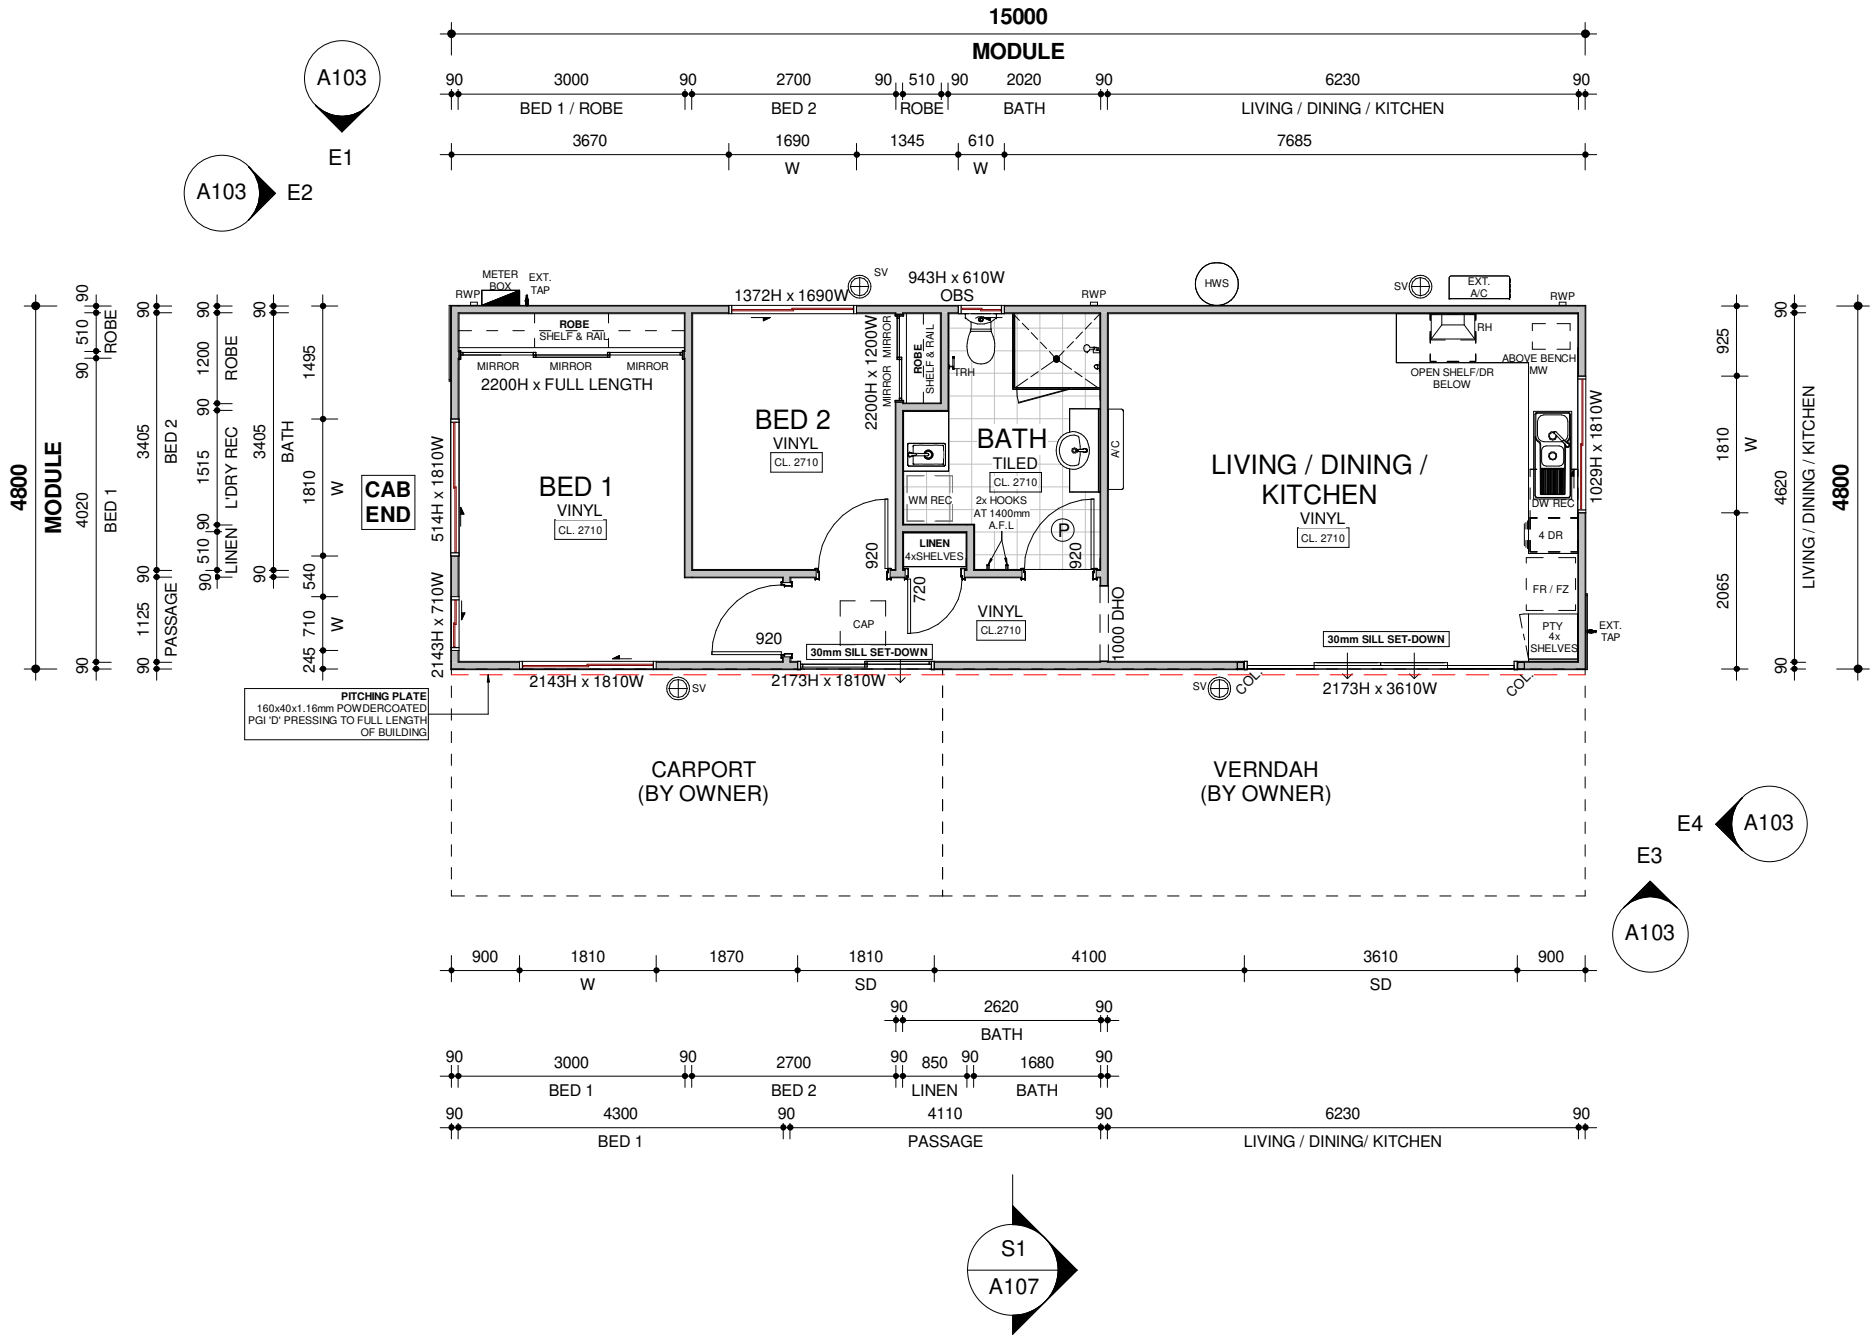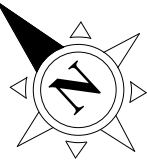

AREA	
BUILDING	72.00m²
VERANDAH	N/A
CARPORT	N/A
PERGOLA	N/A
TOTAL	72.00m²

ROOF AREA	
ROOF (YARD BUILT)	70.19m²
ROOF (SITE BUILT)	N/A
TOTAL	70.19m²

1 FLOOR PLAN
A102 1 : 100

CLIENT: PROPERTY FRIENDS PTY LTD

ADDRESS: LOT 91 BROWNLIE STREET,
WAGGRAKINE WA 6530

HOUSE TYPE: INDICATIVE - 2x1 DWELLING


Rev	Description	Date
0	Issued for construction	28/05/26

JOB No.	25278
DATE:	28/05/2026 10:20:21 AM
DRAWN:	BT
CHECKED:	WI
REV:	SHEET
SCALE:	0
1 : 100	A102




T: 08 64540919 F: 08 64540918
W: modularwa.com.au
e: sales@modularwa.com.au
Builders reg # 101630


Use figured dimensions in preference to scaled.
All dimensions to be verified and checked on the job. © .

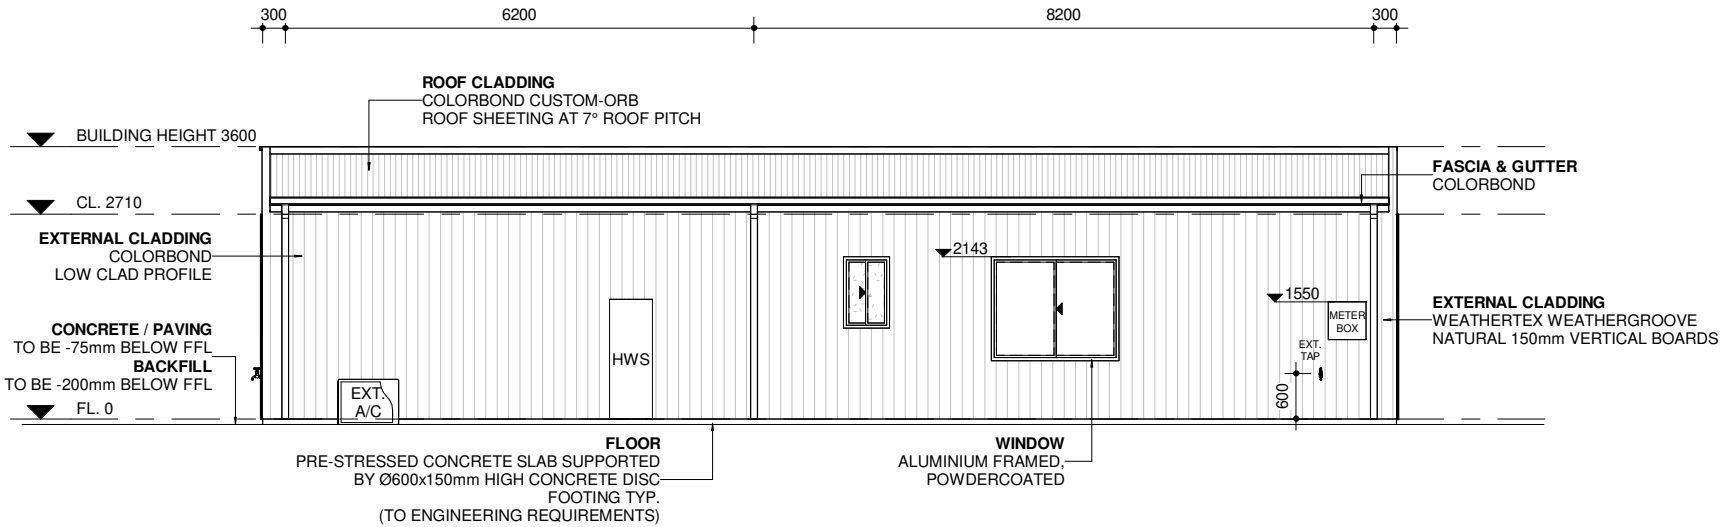


E1 E1 ELEVATION
A103 1 : 100

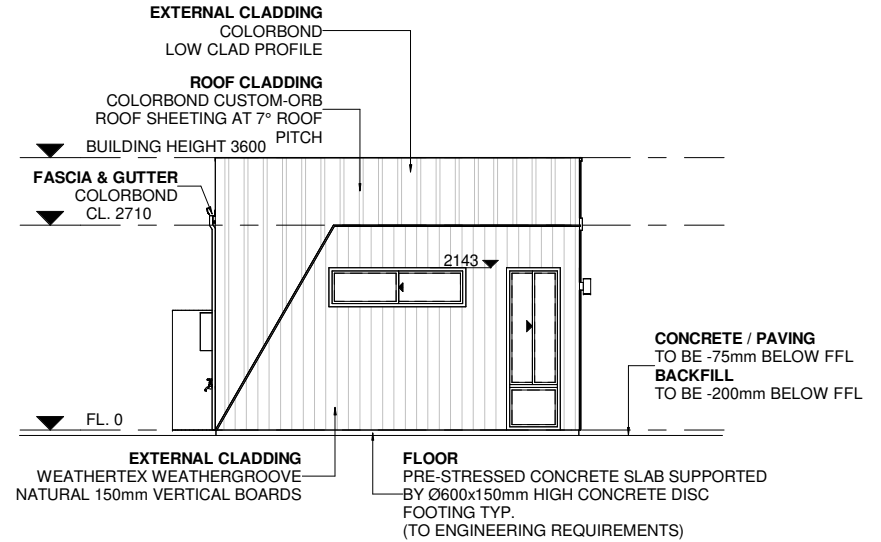

E2 E2 ELEVATION
A103 1 : 100

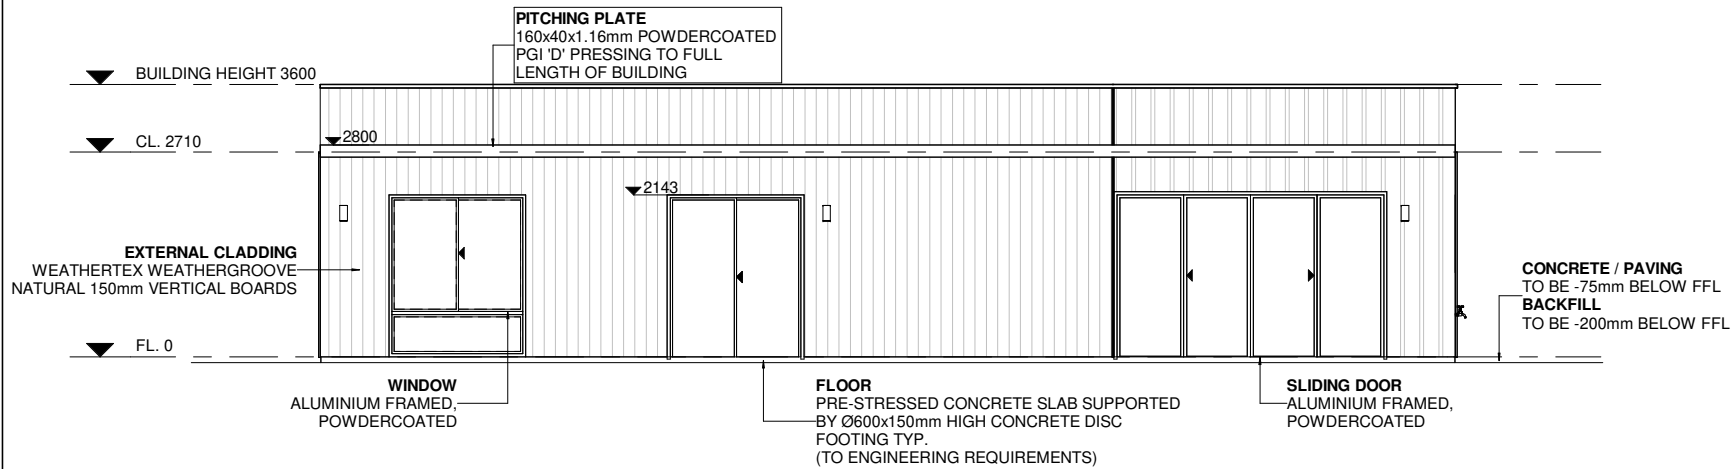

E3 E3 ELEVATION
A103 1 : 100

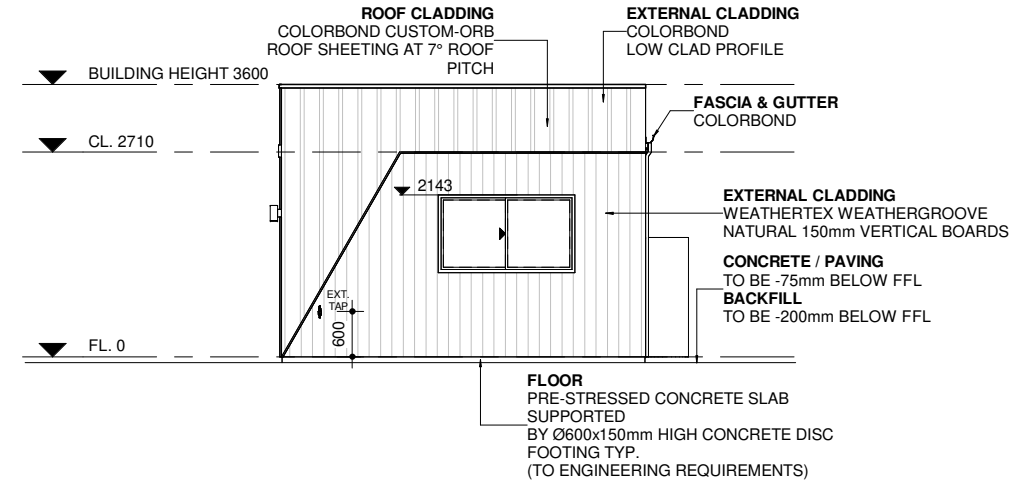

E4 E4 ELEVATION
A103 1 : 100

CLIENT:	PROPERTY FRIENDS PTY LTD	<table><tr><th>Rev</th><th>Description</th><th>Date</th></tr><tr><td>0</td><td>Issued for construction</td><td>28/05/26</td></tr><tr><td> </td><td> </td><td> </td></tr><tr><td> </td><td> </td><td> </td></tr><tr><td> </td><td> </td><td> </td></tr><tr><td> </td><td> </td><td> </td></tr></table>	Rev	Description	Date	0	Issued for construction	28/05/26													JOB No.	25278	 T: 08 64540919 F: 08 64540918 W: modularwa.com.au e: sales@modularwa.com.au Builders reg # 101630 Use figured dimensions in preference to scaled. All dimensions to be verified and checked on the job. © .
Rev	Description		Date																				
0	Issued for construction		28/05/26																				
ADDRESS:	LOT 91 BROWNLIE STREET, WAGGRAKINE WA 6530	DATE:	28/05/2026 10:20:21 AM																				
HOUSE TYPE:	INDICATIVE - 2x1 DWELLING	DRAWN:	BT																				
		CHECKED:	WI																				
		REV:	SHEET																				
		SCALE:	0 1 : 100	A103																			


ELECTRICAL LEGEND	
	CEILING LIGHT - L.E.D OYSTER FITTING
	CEILING LIGHT - L.E.D DOWNLIGHT FITTING
	CEILING LIGHT - L.E.D PENDANT FITTING
	EXTERNAL WALL LIGHT
	EXTERNAL WALL LIGHT - UP/DOWN
	EXTERNAL FLOOD LIGHT - WITH SENSOR
	L.E.D. SURFACE MOUNTED BATTEN
	MOTION SENSOR
	SINGLE GPO
	DOUBLE GPO
	DOUBLE GPO c/w USB OUTLET
	QUAD GPO
	SINGLE WEATHERPROOF GPO
	DOUBLE WEATHERPROOF GPO
	ISOLATION SWITCH
	ISOLATION SWITCH c/w SGPO ON SINGLE SWITCH PLATE
	AIR CONDITIONER UNIT ISOLATOR
	PHONE / DATA OUTLET
	TV POINT
	LIGHT SWITCH
	CLIPSAL FIRETEK 755PSMA4 HARDWIRED SMOKE DETECTOR c/w BATTERY BACKUP AS SHOWN
	EXHAUST FAN FLUMED
	HEAT / LIGHT / FAN
	VENTAIR AIRBUS 250mm ROUND WHITE WITH L.E.D EXHAUST FAN/LIGHT COMBO AS SHOWN
	METER BOX
	GAS NEGUS - NOT APPLICABLE TO THIS PROJECT

ELECTRICAL NOTES:

1. ALL ELECTRICAL HEIGHTS ARE MEASURED FROM FINISHED FLOOR LEVEL.
2. ALL LIGHT SWITCHES TO BE 1200mm ABOVE FINISHED FLOOR LEVEL UNLESS OTHERWISE NOTED.
3. INTERNAL GENERAL POWER OUTLETS, PHONE & DATA POINTS TO BE 300mm ABOVE FINISHED FLOOR LEVEL UNLESS OTHERWISE NOTED.
4. EXTERNAL GENERAL POWER OUTLETS AND EXTERNAL ISO SWITCH TO BE 1200mm ABOVE FINISHED FLOOR LEVEL UNLESS OTHERWISE NOTED.
5. EXTERNAL LIGHT FITTINGS TO BE 1900mm ABOVE FINISHED FLOOR LEVEL - MEASURED TO UNDERSIDE OF FITTING.
6. POWER TO DISHWASHER RECESS, ELECTRIC OVEN, RANGEHOOD, HOT PLATE, HOT WATER SYSTEM.
7. ISOLATOR SWITCH TO BE ABOVE WATER INLET/OUTLET PIPE OF HOUSE AT 1200mm ABOVE FINISHED FLOOR LEVEL.

AIR CONDITIONING NOTE:

1. ALL EXTERNAL A/C BOOTS TO BE LOCATED MIN. 400mm ABOVE FFL.

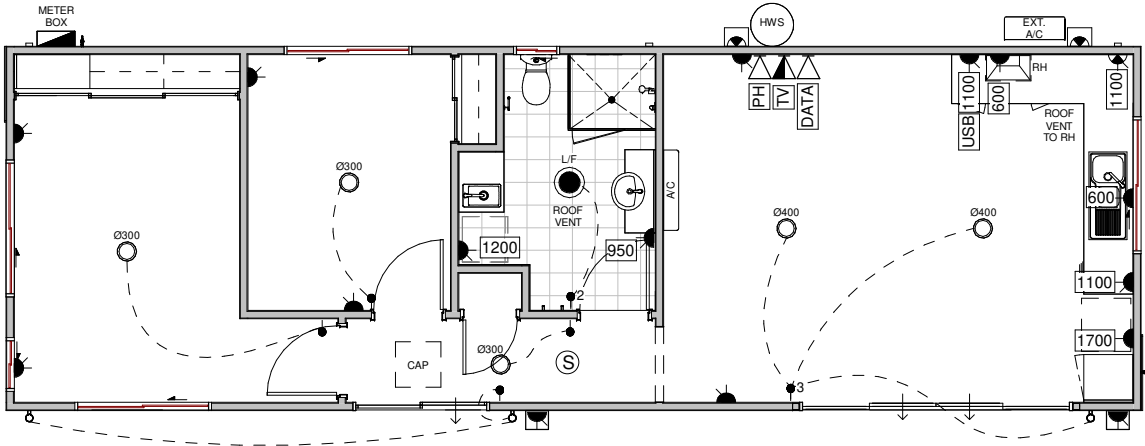

1 ELECTRICAL PLAN
A104 1 : 100


CLIENT:	PROPERTY FRIENDS PTY LTD	<table><tr><th>Rev</th><th>Description</th><th>Date</th></tr><tr><td>0</td><td>Issued for construction</td><td>28/05/26</td></tr><tr><td> </td><td> </td><td> </td></tr><tr><td> </td><td> </td><td> </td></tr><tr><td> </td><td> </td><td> </td></tr></table>	Rev	Description	Date	0	Issued for construction	28/05/26										JOB No.	25278	 T: 08 64540919 F: 08 64540918 W: modularwa.com.au e: sales@modularwa.com.au Builders reg # 101630
Rev	Description		Date																	
0	Issued for construction		28/05/26																	
ADDRESS:	LOT 91 BROWNLIE STREET, WAGGRAKINE WA 6530	DATE:	28/05/2026 10:20:21 AM																	
HOUSE TYPE:	INDICATIVE - 2x1 DWELLING	DRAWN:	BT																	
		CHECKED:	WI																	
		REV:	SHEET																	
		SCALE:	0 1 : 100	A104	Use figured dimensions in preference to scaled. All dimensions to be verified and checked on the job. © .															

**NOTE:
OWNER TO SUPPLY & INSTALL
PORTABLE HOT PLATE**


**NO HANDLES TO DRAWERS, CUPBOARDS & OHC.
REFER TO CUPBOARD FINGER GRIP DETAIL 'FG'**

NOTE:


**DIMENSIONS SHOWN ARE
FROM INTERNAL WALL LINING**

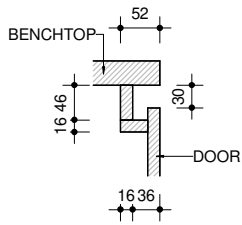


FG CUPBOARD FINGER GRIP DETAIL
A105 1 : 10

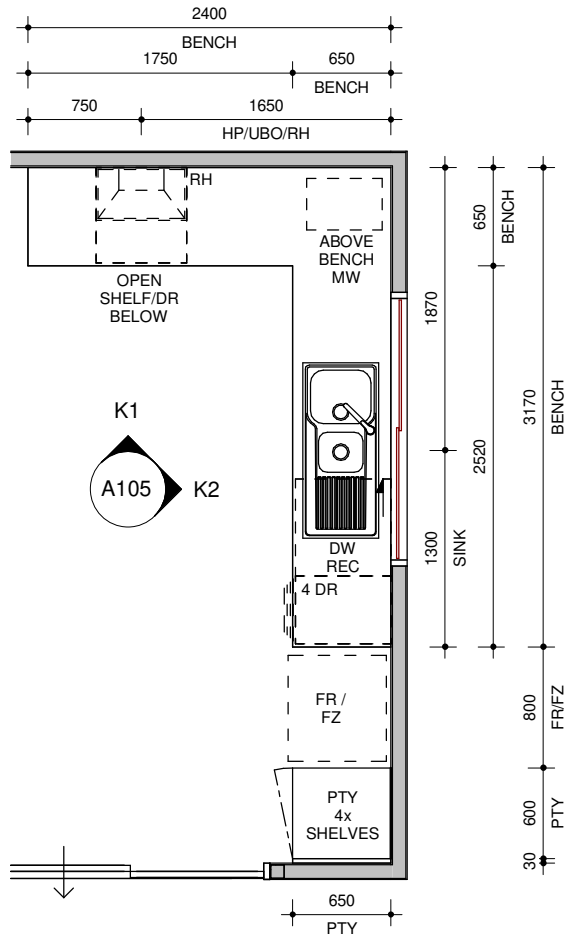

KITCHEN LAYOUT

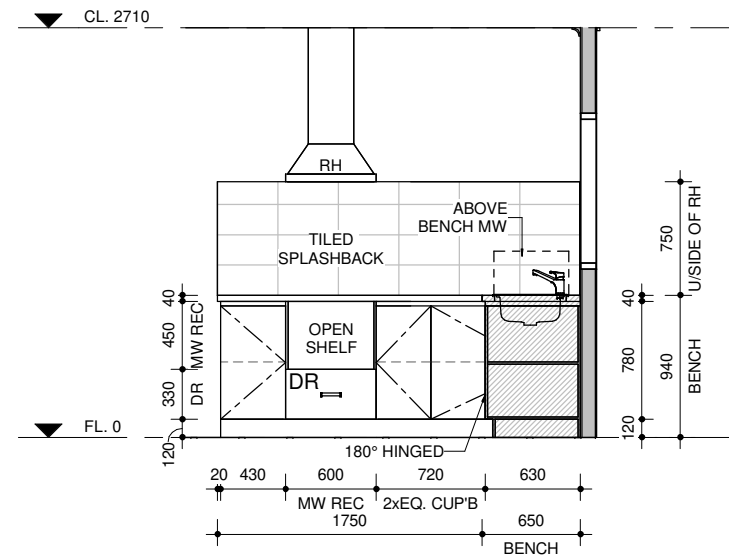

K1 KITCHEN
A105 1 : 50

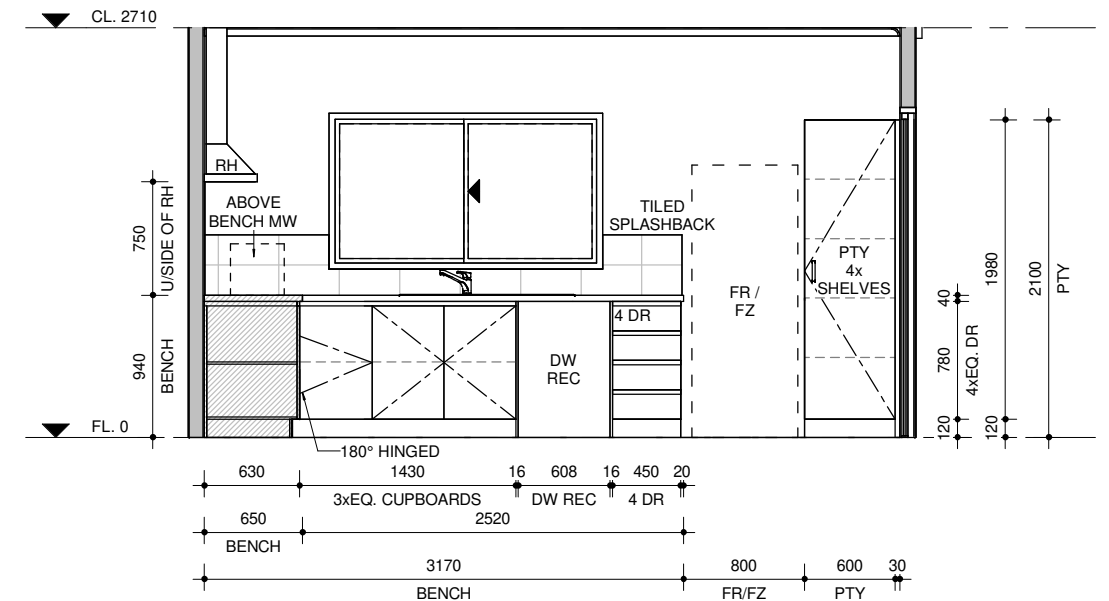


K2 KITCHEN
A105 1 : 50


CLIENT:	PROPERTY FRIENDS PTY LTD	<table><tr><th>Rev</th><th>Description</th><th>Date</th></tr><tr><td>0</td><td>Issued for construction</td><td>28/05/26</td></tr><tr><td></td><td></td><td></td></tr><tr><td></td><td></td><td></td></tr><tr><td></td><td></td><td></td></tr><tr><td></td><td></td><td></td></tr><tr><td></td><td></td><td></td></tr></table>	Rev	Description	Date	0	Issued for construction	28/05/26																JOB No.	25278	 T: 08 64540919 F: 08 64540918 W: modularwa.com.au e: sales@modularwa.com.au Builders reg # 101630 Use figured dimensions in preference to scaled. Copyright All dimensions to be verified and checked on the job. © .
Rev	Description		Date																							
0	Issued for construction		28/05/26																							
ADDRESS:	LOT 91 BROWNLIE STREET, WAGGRAKINE WA 6530	DATE:	28/05/2026 10:20:22 AM																							
HOUSE TYPE:	INDICATIVE - 2x1 DWELLING	DRAWN:	BT																							
		CHECKED:	WI																							
		REV:	SHEET																							
		SCALE:	0																							
		As indicated	A105																							

NO HANDLES TO DRAWERS, CUPBOARDS & OHC.
REFER TO DWG. A105 FOR CUPBOARD
FINGER GRIP DETAIL 'FG'


NOTE:
DIMENSIONS SHOWN ARE
FROM INTERNAL WALL LINING

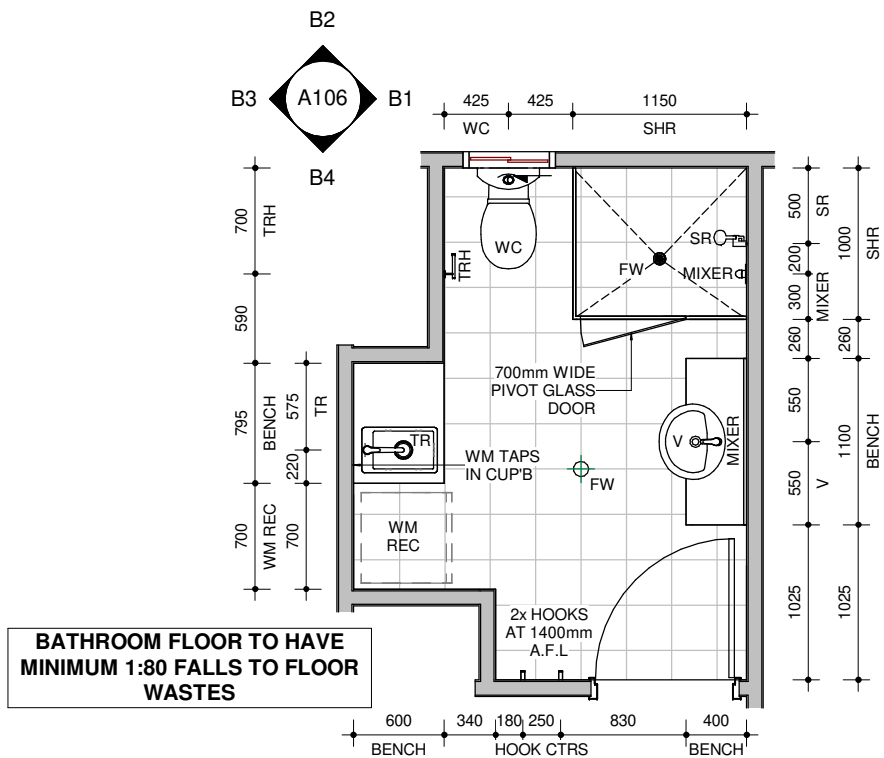


B BATH LAYOUT
A106 1 : 50

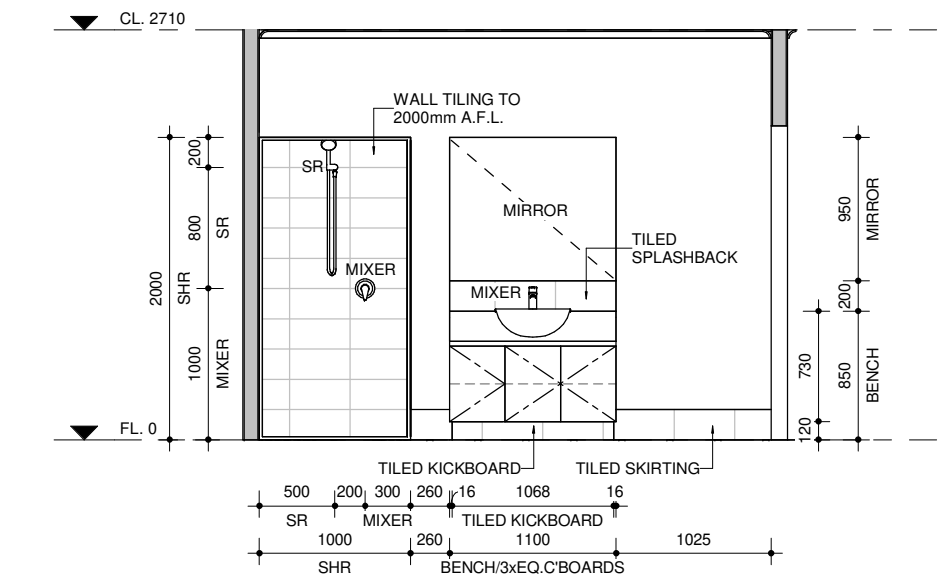


B1 B1 BATH
A106 1 : 50

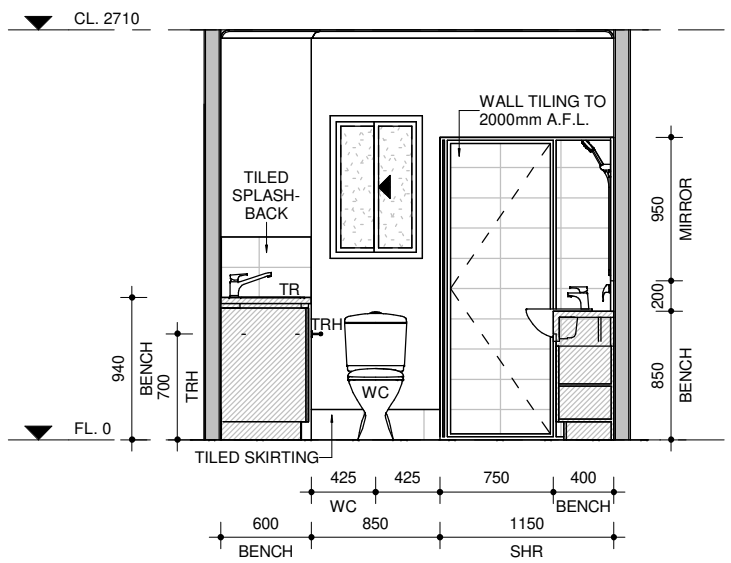

B2 B2 BATH
A106 1 : 50

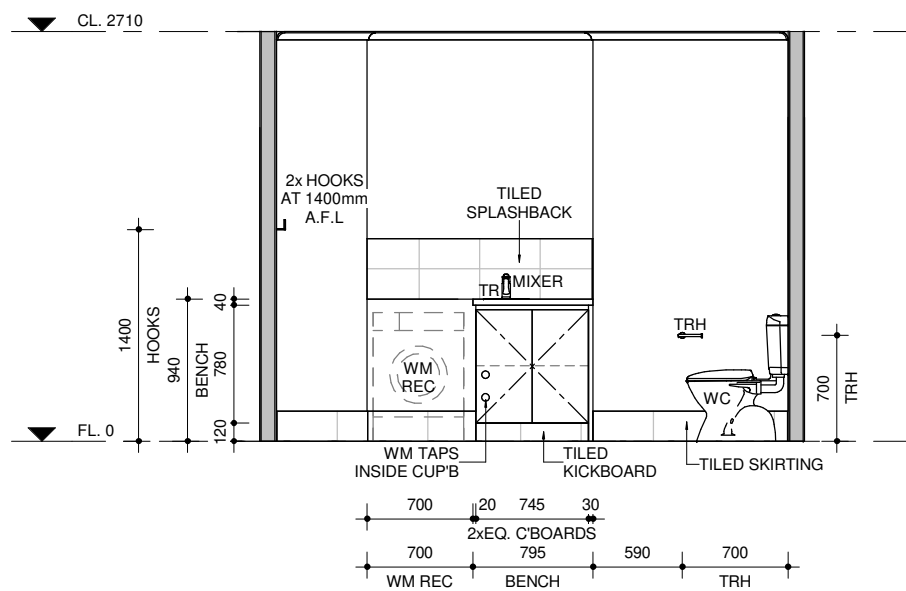

B3 B3 BATH
A106 1 : 50

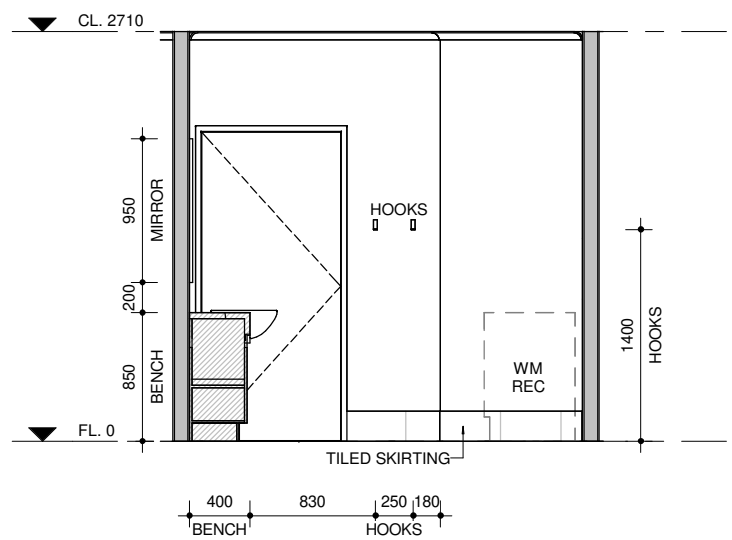

B4 B4 BATH
A106 1 : 50

CLIENT:	PROPERTY FRIENDS PTY LTD
ADDRESS:	LOT 91 BROWNLIE STREET, WAGGRAKINE WA 6530
HOUSE TYPE:	INDICATIVE - 2x1 DWELLING


Rev	Description	Date
0	Issued for construction	28/05/26

JOB No.	25278
DATE:	28/05/2026 10:20:22 AM
DRAWN:	BT
CHECKED:	WI
REV:	SHEET
SCALE:	0
	1 : 50


 **modularwa**

T: 08 64540919 F: 08 64540918
W: modularwa.com.au
e: sales@modularwa.com.au
Builders reg # 101630


Use figured dimensions in preference to scaled.
All dimensions to be verified and checked on the job. © .

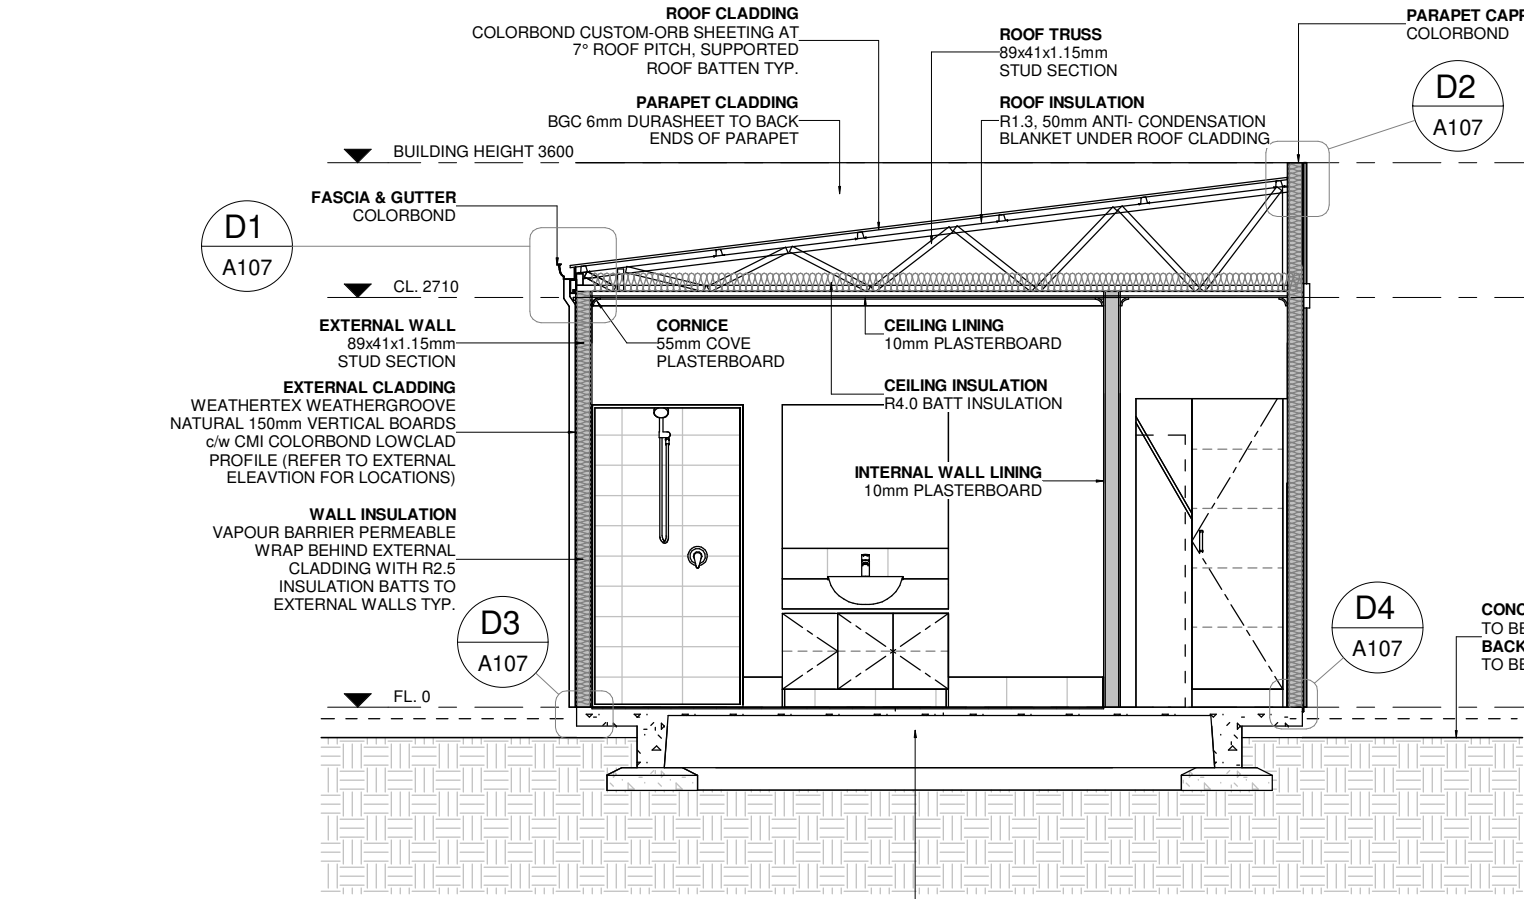


S1 BUILDING SECTION
A107 1 : 50

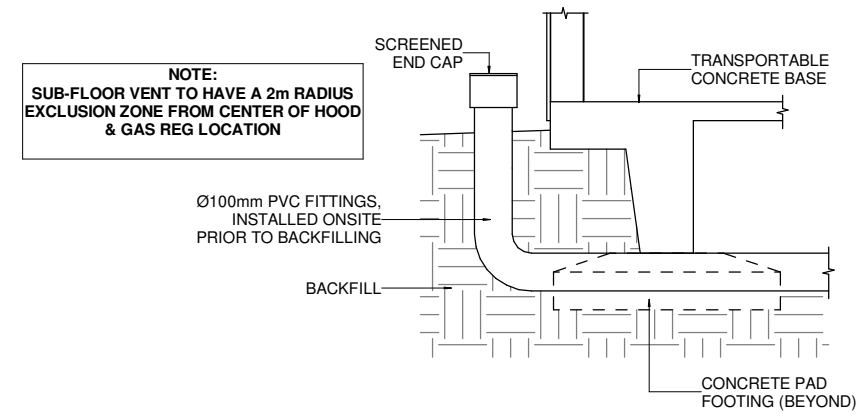


SV SUB FLOOR VENTILATION
A107 1 : 20

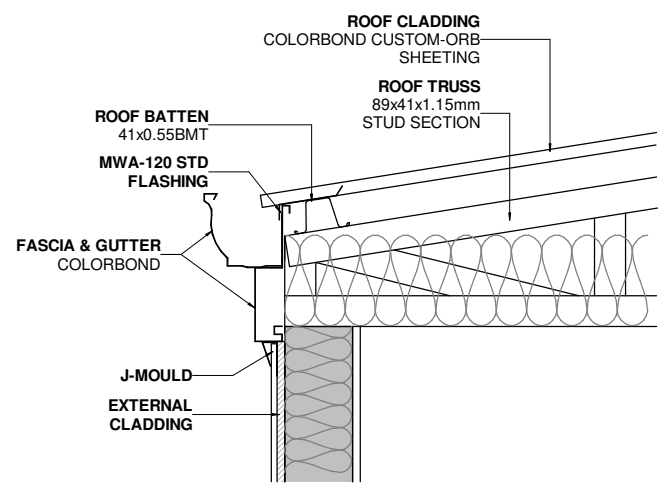


D1 GUTTER DETAIL
A107 1 : 10

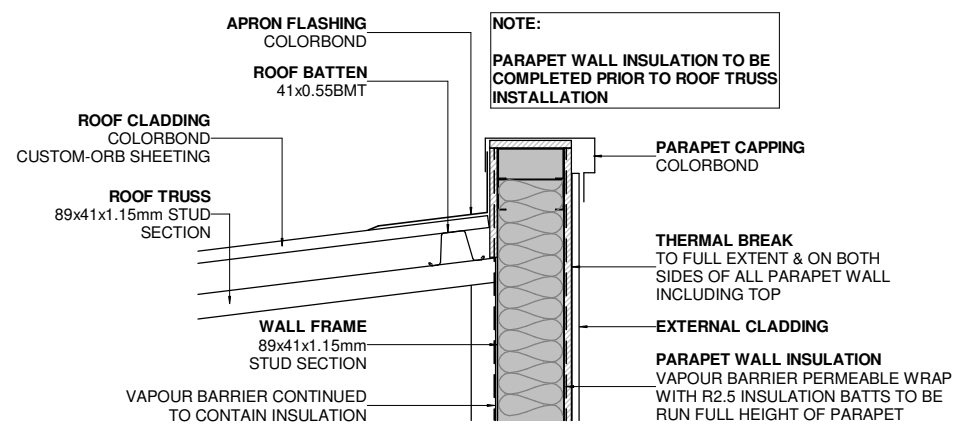

D2 PARAPET DETAIL
A107 1 : 10

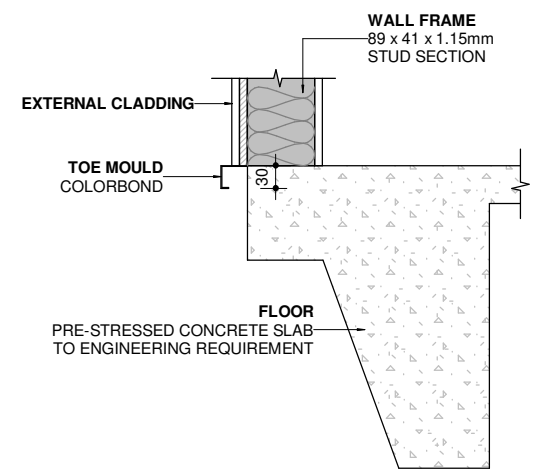

D3 TOE MOULD DETAIL
A107 1 : 10

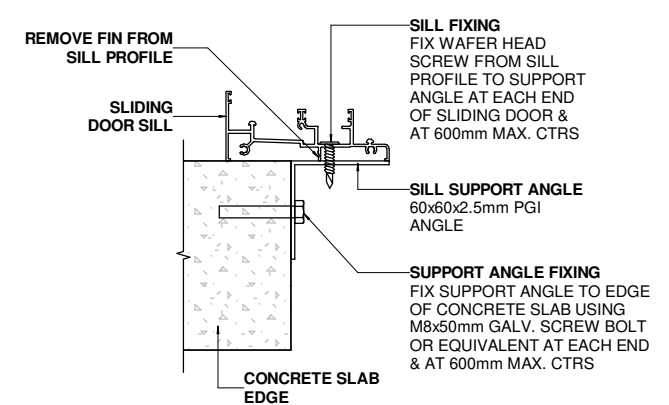

D4 SLIDING DOOR SILL SUPPORT DETAIL
A107 1 : 5


CLIENT:	PROPERTY FRIENDS PTY LTD	<table><tr><th>Rev</th><th>Description</th><th>Date</th></tr><tr><td>0</td><td>Issued for construction</td><td>28/05/26</td></tr><tr><td> </td><td> </td><td> </td></tr><tr><td> </td><td> </td><td> </td></tr><tr><td> </td><td> </td><td> </td></tr></table>	Rev	Description	Date	0	Issued for construction	28/05/26										JOB No.	25278	 T: 08 64540919 F: 08 64540918 W: modularwa.com.au e: sales@modularwa.com.au Builders reg # 101630 Use figured dimensions in preference to scaled. All dimensions to be verified and checked on the job. © .
Rev	Description		Date																	
0	Issued for construction		28/05/26																	
ADDRESS:	LOT 91 BROWNLIE STREET, WAGGRAKINE WA 6530	DATE:	28/05/2026 10:20:23 AM																	
HOUSE TYPE:	INDICATIVE - 2x1 DWELLING	DRAWN:	BT																	
		CHECKED:	WI																	
		REV:	SHEET																	
		SCALE:	0	A107																
		As indicated																		

FOUNDATION NOTES:

1. FOUNDATION SOIL TO BE CLEAN, COMPACT, NATURAL GROUND, FREE OF EXCESSIVE MOISTURE.
2. GROUND SHALL BE COMPACTED TO ACHIEVE: FOR SAND SITES, MINIMUM 6 BLOWS OVER 150-450 MM, 7 BLOWS OVER 450-750 MM, AND 9 BLOWS OVER 750-1050 MM WITH A PERTH SAND PENETROMETER (AS1289.6.3.3) FOR COHESIVE/GRAVEL SITES, MINIMUM 6 BLOWS OVER 150MM USING A DYNAMIC CONE PENETROMETER (DCP) THROUGH ALL FILL OR TO 600MM IN NATURAL GROUND.
3. PREPARE SITE SUCH THAT SURFACE RUNOFF CANNOT DRAIN OVER OR UNDER FOUNDATIONS.
4. FOOTING HAS BEEN DESIGNED FOR SOIL CLASS "TBC"

DO NOT SCALE FROM THIS DRAWING
ALL CONTRACTORS TO CHECK DIMENSIONS AND NOTES PRIOR TO COMMENCEMENT OF ANY WORKS AND ANY DISCREPANCIES TO BE NOTIFIED TO THE SITE SUPERVISOR WITHOUT DELAY.

PENETRATIONS		
CIP	CAST IN PLATE	150 SQ
FW	FLOOR WASTE	65Ø
VB	VANITY BASIN	65Ø
KS	KITCHEN SINK	65Ø
TR	TROUGH	65Ø
WC	WC PAN	125Ø
SHR	SHOWER WASTE	125Ø

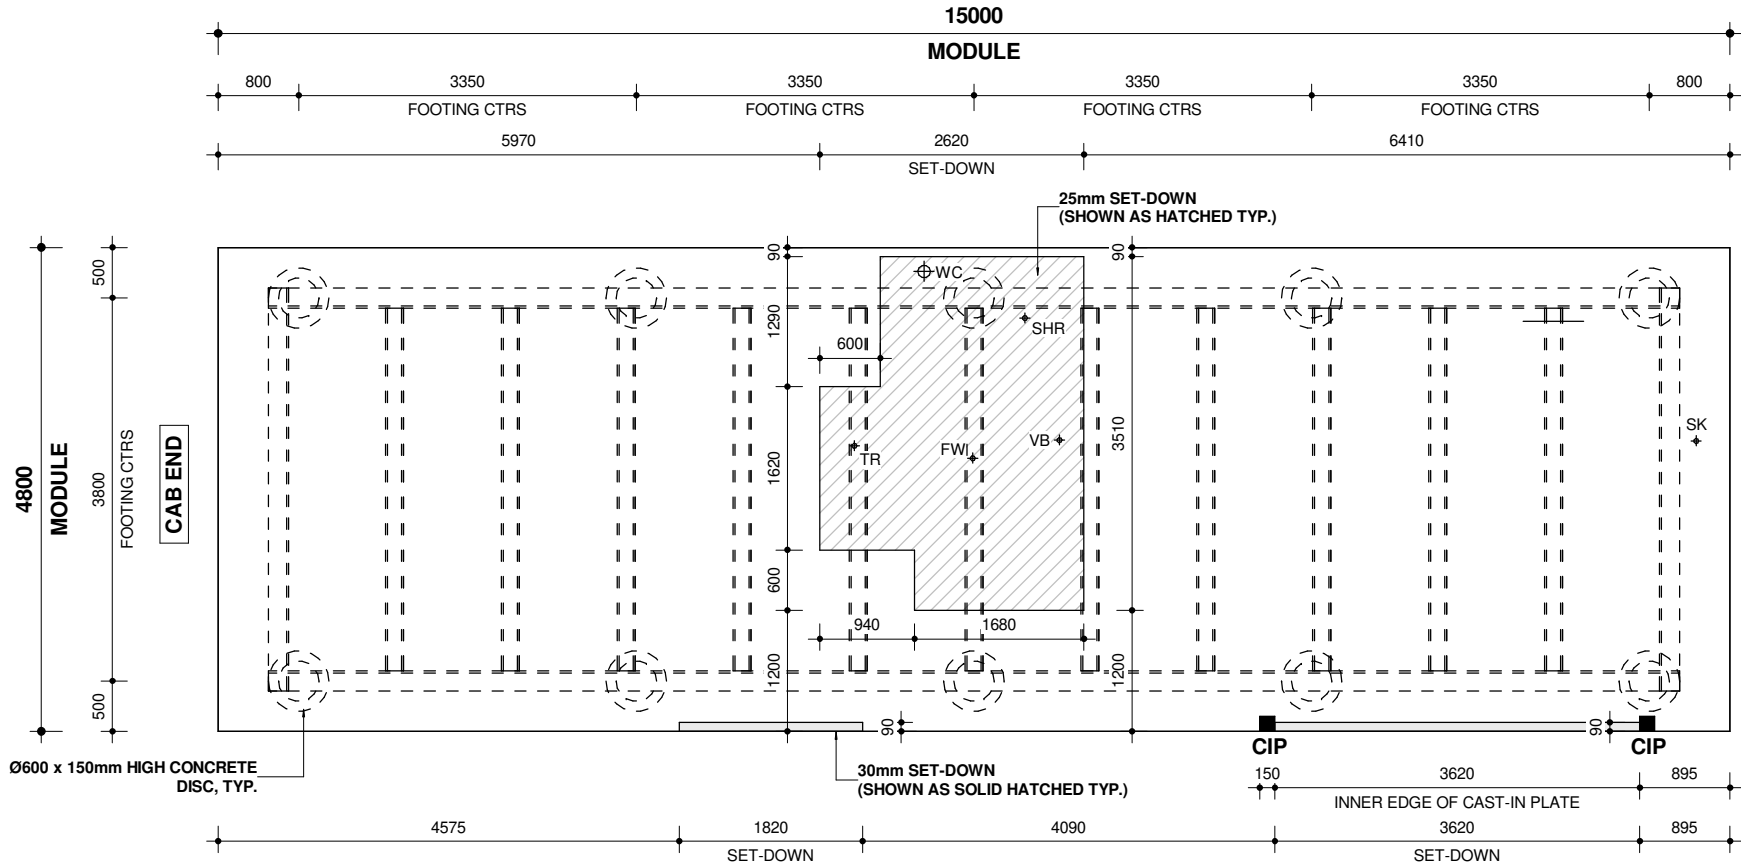

1 CONCRETE SLAB PLAN
A108 1 : 75

CLIENT:	PROPERTY FRIENDS PTY LTD	<table><tr><th>Rev</th><th>Description</th><th>Date</th></tr><tr><td>0</td><td>Issued for construction</td><td>28/05/26</td></tr><tr><td> </td><td> </td><td> </td></tr><tr><td> </td><td> </td><td> </td></tr><tr><td> </td><td> </td><td> </td></tr><tr><td> </td><td> </td><td> </td></tr><tr><td> </td><td> </td><td> </td></tr><tr><td> </td><td> </td><td> </td></tr></table>	Rev	Description	Date	0	Issued for construction	28/05/26																			JOB No.	25278	 T: 08 64540919 F: 08 64540918 W: modularwa.com.au e: sales@modularwa.com.au Builders reg # 101630 Use figured dimensions in preference to scaled. All dimensions to be verified and checked on the job. © .
Rev	Description		Date																										
0	Issued for construction		28/05/26																										
ADDRESS:	LOT 91 BROWNLIE STREET, WAGGRAKINE WA 6530	DATE:	28/05/2026 10:20:23 AM																										
HOUSE TYPE:	INDICATIVE - 2x1 DWELLING	DRAWN:	BT																										
		CHECKED:	WI																										
		REV:	SHEET																										
		SCALE:	0 As indicated	A108																									