

BAL-12.5 TO AS3959-2018
CONSTRUCTION NOTES

TO COMPLY WITH SECTION 3 AND 5 OF AS3959-2018 INCLUDING BUT NOT LIMITED TO THE FOLLOWING:

FLOOR
CONCRETE SLAB ON GROUND

EXTERNAL WALLS
90mm THICK STEEL STUD SECTIONS

JOINTS
ALL JOINTS IN THE EXTERNAL SURFACE MATERIAL OF WALLS SHALL BE COVERED, SEALED, OVERLAPPED, BACKED OR BUTT-JOINTED TO PREVENT GAPS.

VENTS AND WEEPHOLES
VENTS AND WEEPHOLES IN EXTERNAL WALLS SHALL BE SCREENED WITH ALUMINIUM MESH WITH A MAXIMUM APERTURE OF 2mm.

SCREENS FOR WINDOWS & DOORS
ALUMINIUM MESH SCREEN WITH A MAX. APERTURE OF 2mm AND BE TIGHT FITTING TO THE WINDOW/DOOR FRAME. FRAME SUPPORTING MESH SHALL BE ALUMINIUM.

WINDOW / GLAZING (UNLESS NOTED OTHERWISE)
POWDER-COATED ALUMINIUM FRAMED. WHERE GLAZING IS LESS THAN 400mm FROM THE GROUND, GLAZING TO BE MIN. 4mm THICK GRADE A SAFETY GLASS. OPENABLE PORTION OF WINDOW TO BE SCREENED EXTERNALLY WITH SCREENS AS DESCRIBED ABOVE.


ROOF
METAL ROOF SHEETING AND ALL ROOF ACCESSORIES TO BE NON-COMBUSTIBLE.

ROOF / WALL AND ROOF / ROOF JUNCTION SHALL BE SEALED OR PROTECTED WITH ALUMINIUM MESH WITH MAX. APERTURE OF 2mm.

ROOF TO BE FULLY SARKED. SARKING SHALL:
• BE LOCATED ON TOP OF ROOF FRAMING, EXCEPT THAT FOIL-BACKED INSULATION MAY BE FIXED ABOVE THE ROOF BATTENS; AND
• COVER THE ENTIRE ROOF INCLUDING THE RIDGE AND HIPS; AND
• EXTEND INTO THE GUTTERS AND VALLEYS.

SHEET ROOFS SHALL HAVE ANY GAPS SEALED AT THE FASCIA OR WALL LINE, HIPS AND RIDGES BY:
• ALUMINIUM MESH WITH MAX. APERTURE OF 2mm; OR
• MINERAL WOOL; OR
• OTHER NON-COMBUSTIBLE MATERIALS; OR
• A COMBINATION OF THE ABOVE ITEMS.


ROOF PENETRATION SUCH AS ROOF VENTS
• SHALL BE FITTED WITH ALUMINIUM EMBER GUARDS WITH MAX. APERTURE OF 2mm.
• SHALL BE SEALED. THE MATERIAL USED TO SEAL THE PENETRATION SHALL BE NON-COMBUSTIBLE.

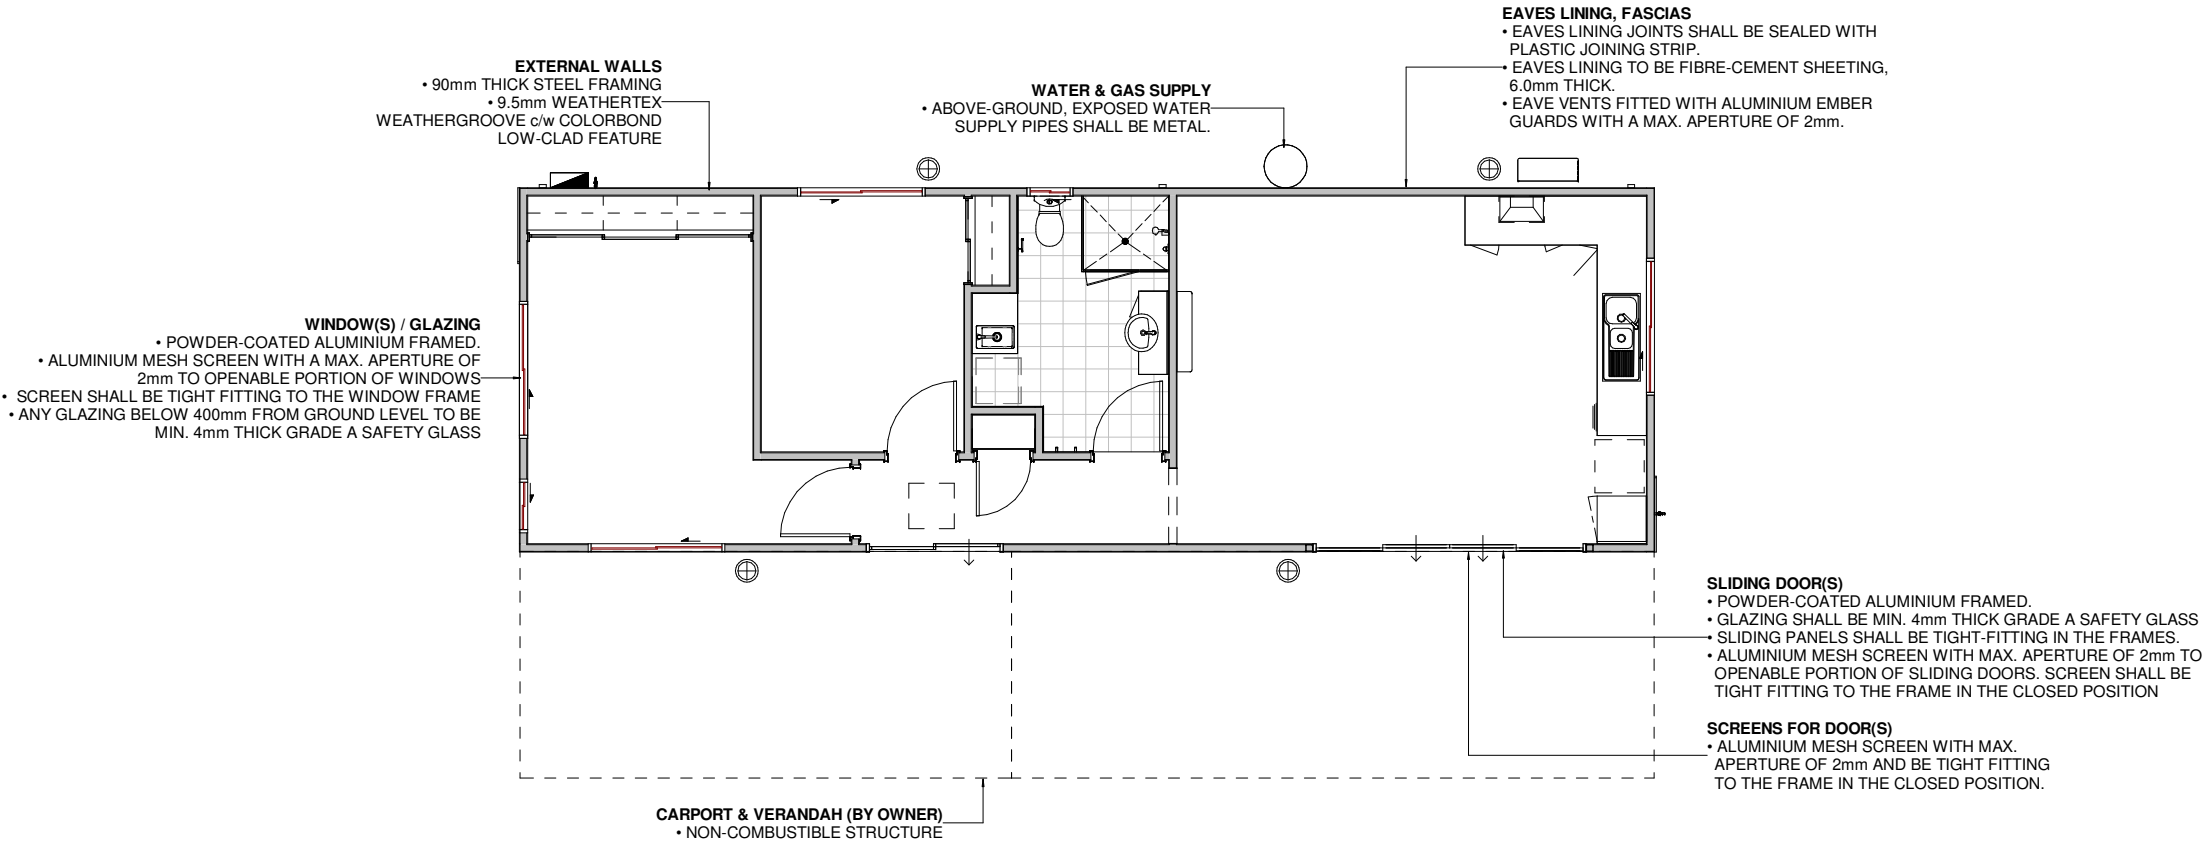

1 BUSHFIRE CONSTRUCTION PLAN
A100 1 : 100


CLIENT:	PROPERTY FRIENDS PTY LTD	<table><tr><th>Rev</th><th>Description</th><th>Date</th></tr><tr><td>F</td><td>Add 4th carbay on site plan</td><td>20/02/26</td></tr><tr><td>G</td><td>Update final plans as per CV-1</td><td>19/03/26</td></tr><tr><td>H</td><td>Updated sliding door height for B2 & concrete slab plan for set-down</td><td>19/03/26</td></tr><tr><td>I</td><td>Relocate MW to above bench, MW recess to become open shelf, add DGPO/USB to kitchen, update DGPO/Isolator in kitchen</td><td>15/04/26</td></tr><tr><td>J</td><td>Add pitching plate to full length of building</td><td>28/04/26</td></tr><tr><td>K</td><td>Update site information</td><td>29/04/26</td></tr></table>	Rev	Description	Date	F	Add 4th carbay on site plan	20/02/26	G	Update final plans as per CV-1	19/03/26	H	Updated sliding door height for B2 & concrete slab plan for set-down	19/03/26	I	Relocate MW to above bench, MW recess to become open shelf, add DGPO/USB to kitchen, update DGPO/Isolator in kitchen	15/04/26	J	Add pitching plate to full length of building	28/04/26	K	Update site information	29/04/26	JOB No.	25278	 T: 08 64540919 F: 08 64540918 W: modularwa.com.au e: sales@modularwa.com.au Builders reg # 101630
Rev	Description		Date																							
F	Add 4th carbay on site plan		20/02/26																							
G	Update final plans as per CV-1		19/03/26																							
H	Updated sliding door height for B2 & concrete slab plan for set-down		19/03/26																							
I	Relocate MW to above bench, MW recess to become open shelf, add DGPO/USB to kitchen, update DGPO/Isolator in kitchen		15/04/26																							
J	Add pitching plate to full length of building		28/04/26																							
K	Update site information	29/04/26																								
ADDRESS:	LOT 91 BROWNLIE STREET, WAGGRAKINE WA 6530	DATE:	29/04/2026 3:15:03 PM																							
HOUSE TYPE:	INDICATIVE - 2x1 DWELLING	DRAWN:	BT																							
		CHECKED:	wi																							
		REV:	SHEET																							
		SCALE:	A100																							
		1 : 100																								
		Use figured dimensions in preference to scaled. Copyright All dimensions to be verified and checked on the job. © .																								

F.F.L - FINISHED FLOOR LEVEL
F.B.L - FINISHED BACKFILL LEVEL
F.C.L - FINISHED CUT/COMPACT LEVEL
N.G.L - NATURAL GROUND LEVEL

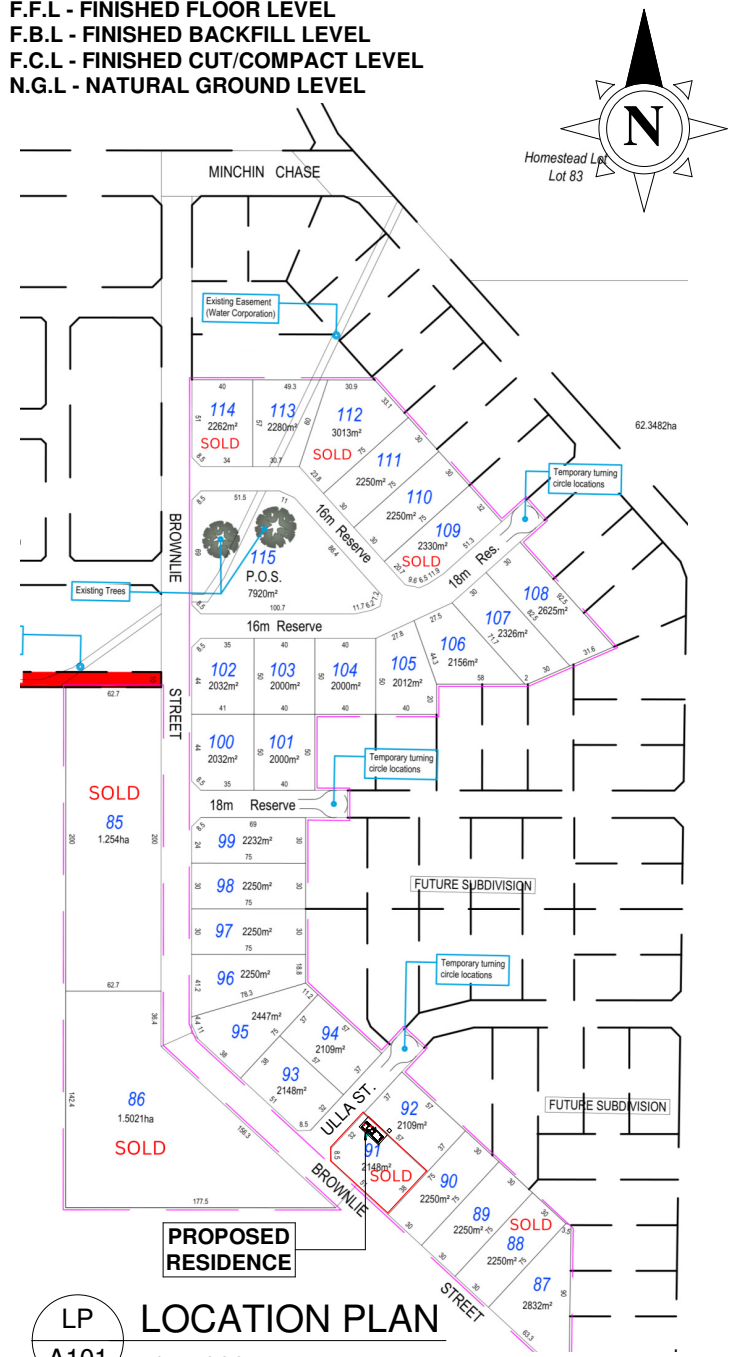

- SITE NOTES:**
1. ALL BOUNDARIES, DIMENSIONS, SETBACKS AND LOCATION OF EXISTING RETAINING TO BE CONFIRMED ON RECEIPT OF SURVEY.
 2. FFL TO BE CONFIRMED ON RECIEPT OF SURVEY.
 3. SITE SERVICES AND LOCATIONS TO BE CONFIRMED ON RECEIPT OF SURVEY.
 4. NO VERGE INFRASTRUCTURE IS PROPOSED ADJACENT TO THIS LOT. THE ONLY PERMANENT SUBDIVISION INFRASTRUCTURE IN THE VICINITY IS THE STORMWATER CULVERT AT THE BROWNLIE STREET / ULLA STREET INTERSECTION — REFER MONTGOMERY ENGINEERING CONSULTANTS DRAWING C212460-R-050 REV 4.

SP A101 SITE PLAN
1 : 250

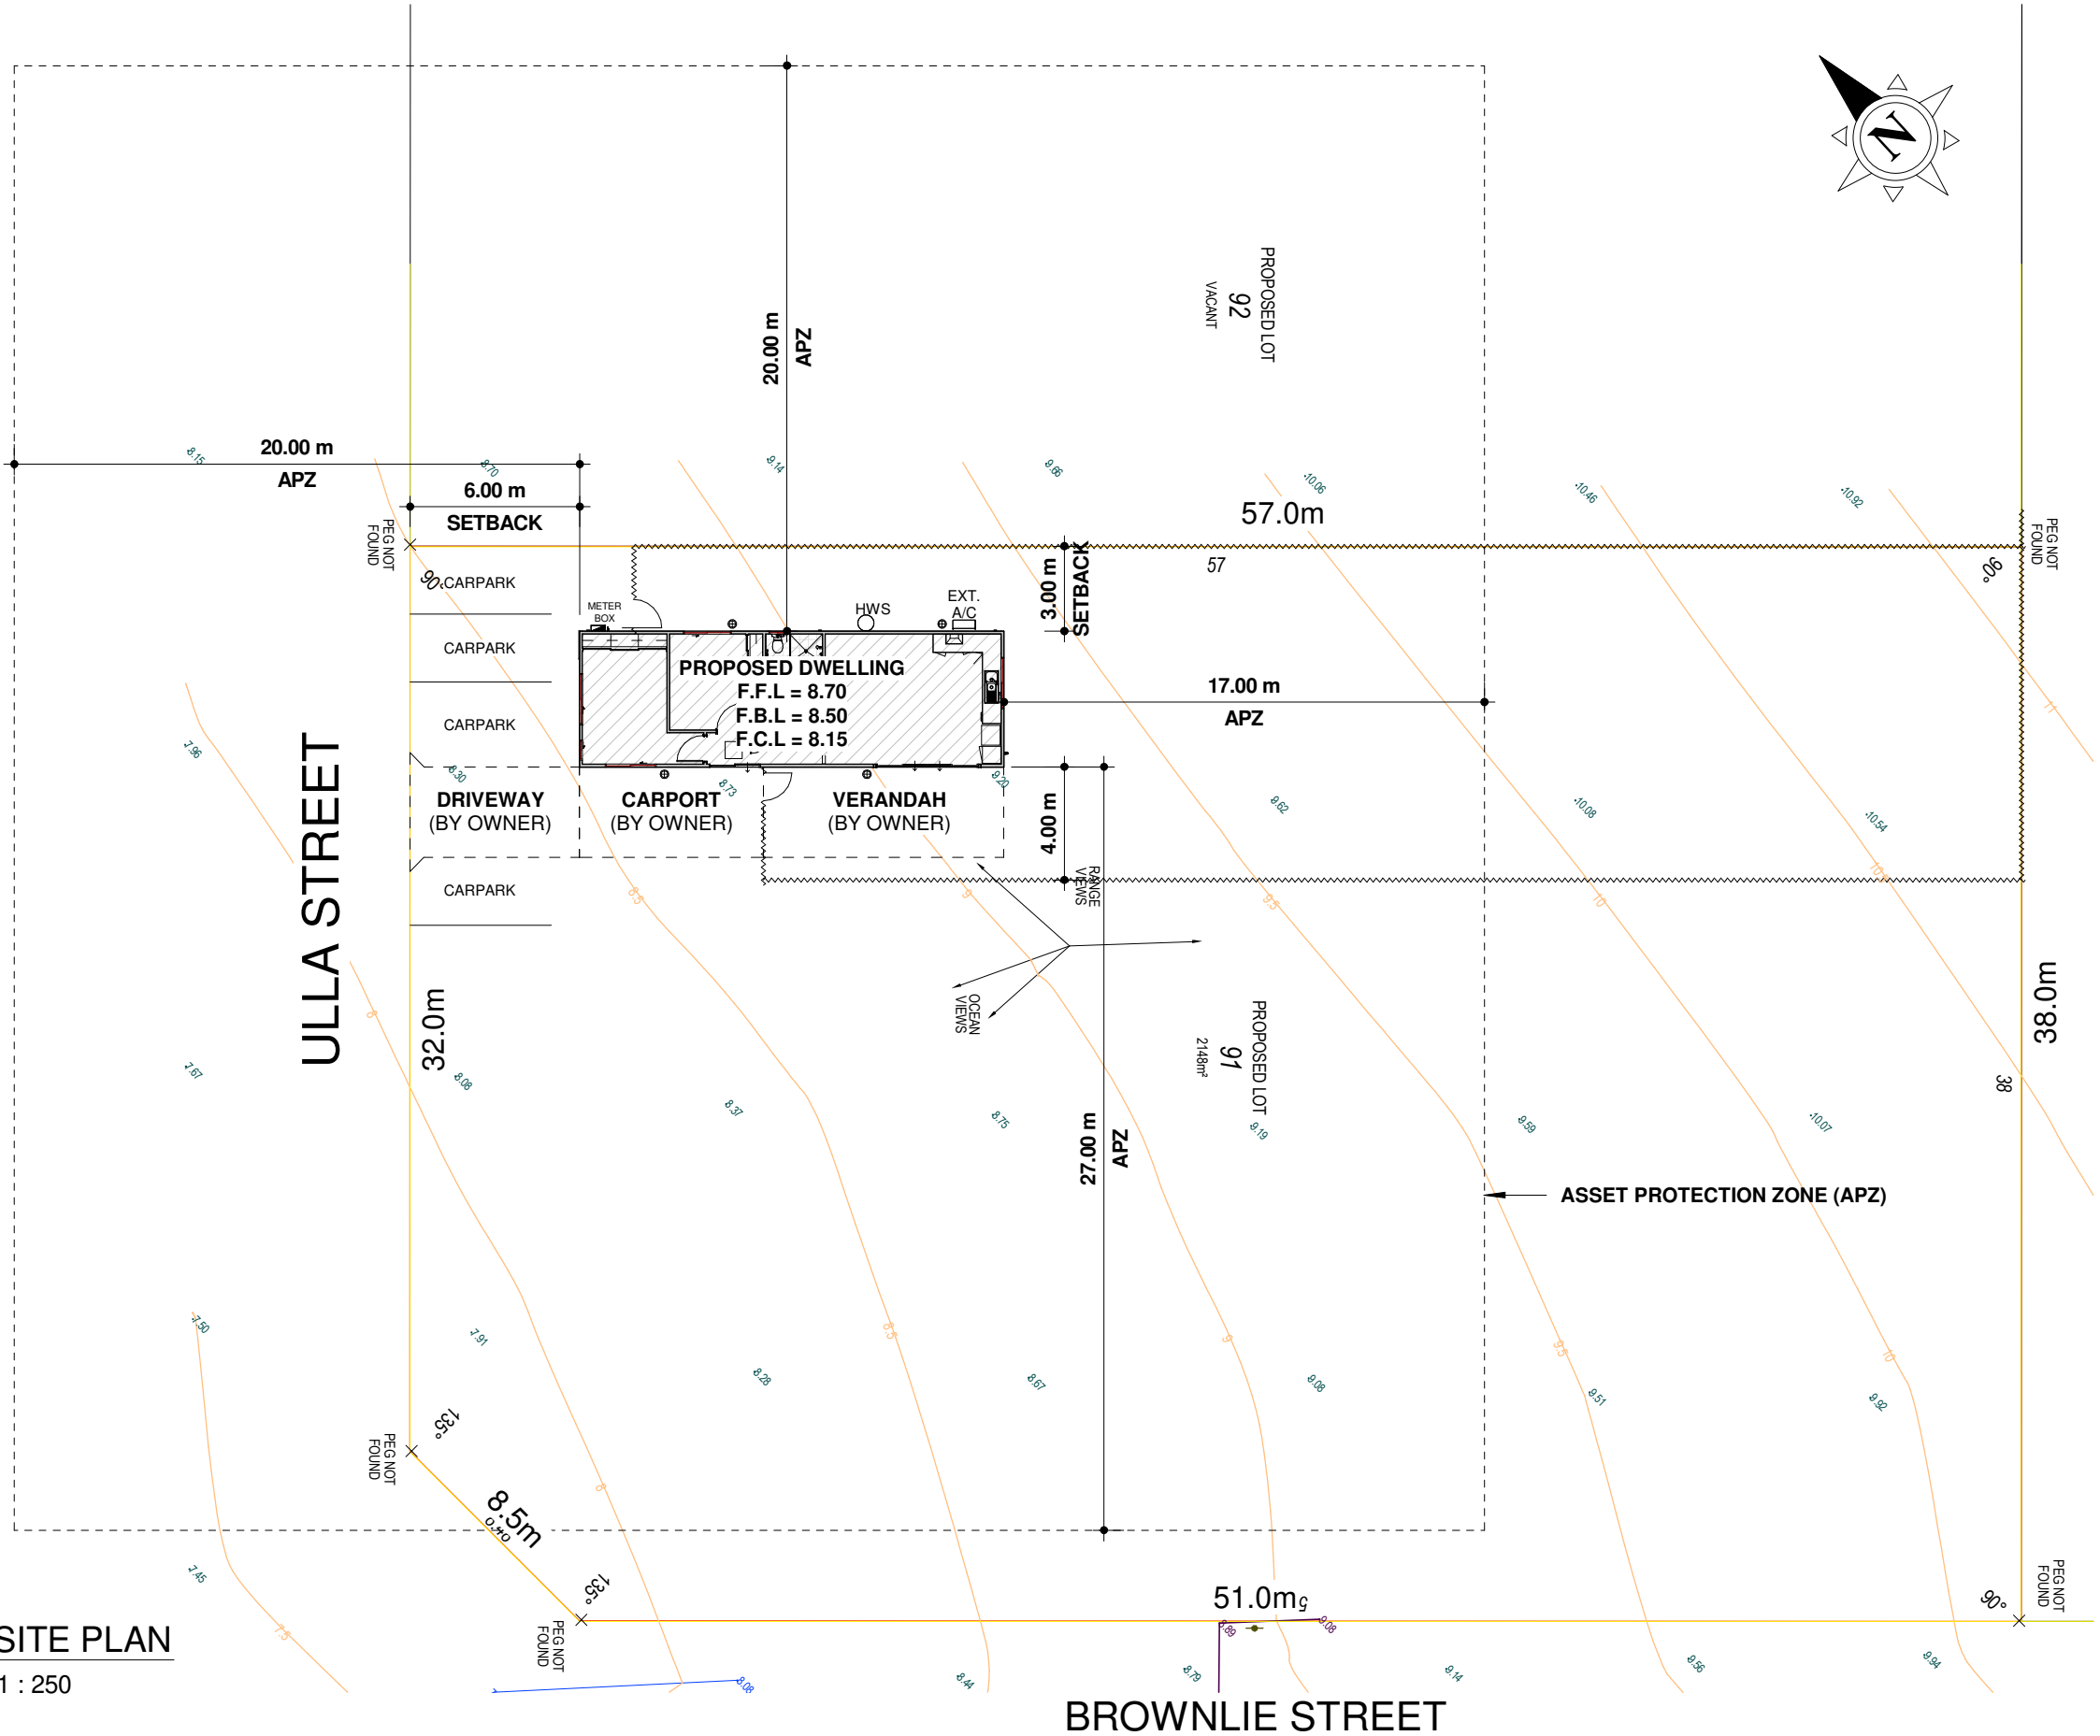

CLIENT:	PROPERTY FRIENDS PTY LTD
ADDRESS:	LOT 91 BROWNLIE STREET, WAGGRAKINE WA 6530
HOUSE TYPE:	INDICATIVE - 2x1 DWELLING

Rev	Description	Date
F	Add 4th carbay on site plan	20/02/26
G	Update final plans as per CV-1	19/03/26
H	Updated sliding door height for B2 & concrete slab plan for set-down	19/03/26
I	Relocate MW to above bench, MW recess to become open shelf, add DGPO/USB to kitchen, update DGPO/Isolator in kitchen	15/04/26
J	Add pitching plate to full length of building	28/04/26
K	Update site information	29/04/26

JOB No.	25278
DATE:	29/04/2026 3:15:04 PM
DRAWN:	BT
CHECKED:	WI
REV:	SHEET
SCALE:	K
As indicated	A101


T: 08 64540919 F: 08 64540918
W: modularwa.com.au
e: sales@modularwa.com.au
Builders reg # 101630
Use figured dimensions in preference to scaled.
All dimensions to be verified and checked on the job. © .

GENERAL NOTES:

1. DO NOT SCALE FROM THIS DRAWING. ALL CONTRACTORS TO CHECK DIMENSIONS AND NOTES PRIOR TO COMMENCEMENT OF ANY WORKS AND ANY DISCREPANCIES TO BE NOTIFIED TO THE SITE SUPERVISOR WITHOUT DELAY.
2. DIMENSIONS SHOWN ON THIS PLAN ARE TO STEEL FRAME AND DOES NOT INCLUDE EXTERNAL CLADDING OR INTERNAL LINING WIDTH.

CLIENT NOTE:

1. THIS PLAN IS TO BE READ IN CONJUNCTION WITH MODULAR WA ADDENDA AND ENGINEERED CERTIFIED DRAWINGS.

2. OWNER TO SUPPLY & INSTALL PORTABLE HOT PLATE. NO ALLOWANCE FOR BUILDER SUPPLIED HOT PLATE.

CARPENTERS NOTE:

SILICONE BEAD REQUIRED AT BASE OF WALL FRAMES TO ALL TILED WET AREAS

INTERNAL OPENINGS:

DHO: FLUSHED DOOR HEIGHT OPENING 2080mm A.F.L
FHO: FULL HEIGHT OPENING

DOORS & WINDOWS

1. WINDOW HEAD HEIGHT TO BE 2143mm A.F.L UNLESS NOTED OTHERWISE.
2. INSTALL SILL SUPPORT ANGLE TO ALL ALUMINIUM EXTERNAL SLIDING DOORS. REFER TO DETAIL.
3. ALL WINDOW & SLIDING DOOR FLYMESH TO BE ALUMINIUM TYPE.
4. NON TRANSPARENT WINDOW BLINDS BY OWNER FOR ENERGY COMPLIANCE.
5. ALL WINDOWS AND EXTERNAL SLIDING DOORS TO BE CYCLONIC RATED TO SUIT REGION B2.



ABBREVIATION LEGEND

HP	HOT PLATE
RH	RANGEHOOD
UBO	UNDERBENCH OVEN
OHC	OVERHEAD CUPBOARD
DR	DRAWER
FR/FZ REC	FRIDGE / FREEZER RECESS
DW REC	DISHWASHER RECESS
TR	TROUGH
WM REC	WASHING MACHINE RECESS
TRH	TOILET ROLL HOLDER
DTR	DOUBLE TOWEL RAIL
TRG	TOWEL RING
SR	SHOWER RAIL / ROSE
CAP	CEILING ACCESS PANEL
BRM	BROOM
V	VANITY
B	BASIN
OBS	OBSCURE
TF	TIMBER FRAME
AF	ALUMINIUM FRAME
SD	SLIDING DOOR
D	DOOR
W	WINDOW
AW	AWNING WINDOW
FW	FIXED WINDOW
COL	COLUMN
H/H	HEAD HEIGHT
RWP	RAIN WATER PIPE
SV	SUB-FLOOR VENT
LOH	LIFT OFF HINGES
Ⓟ	PRIVACY LATCH

BUSHFIRE ATTACK
LEVEL (BAL): 12.5

WIND CLASSIFICATION:
REGION "B2"

SOIL CLASSIFICATION: "TBC"

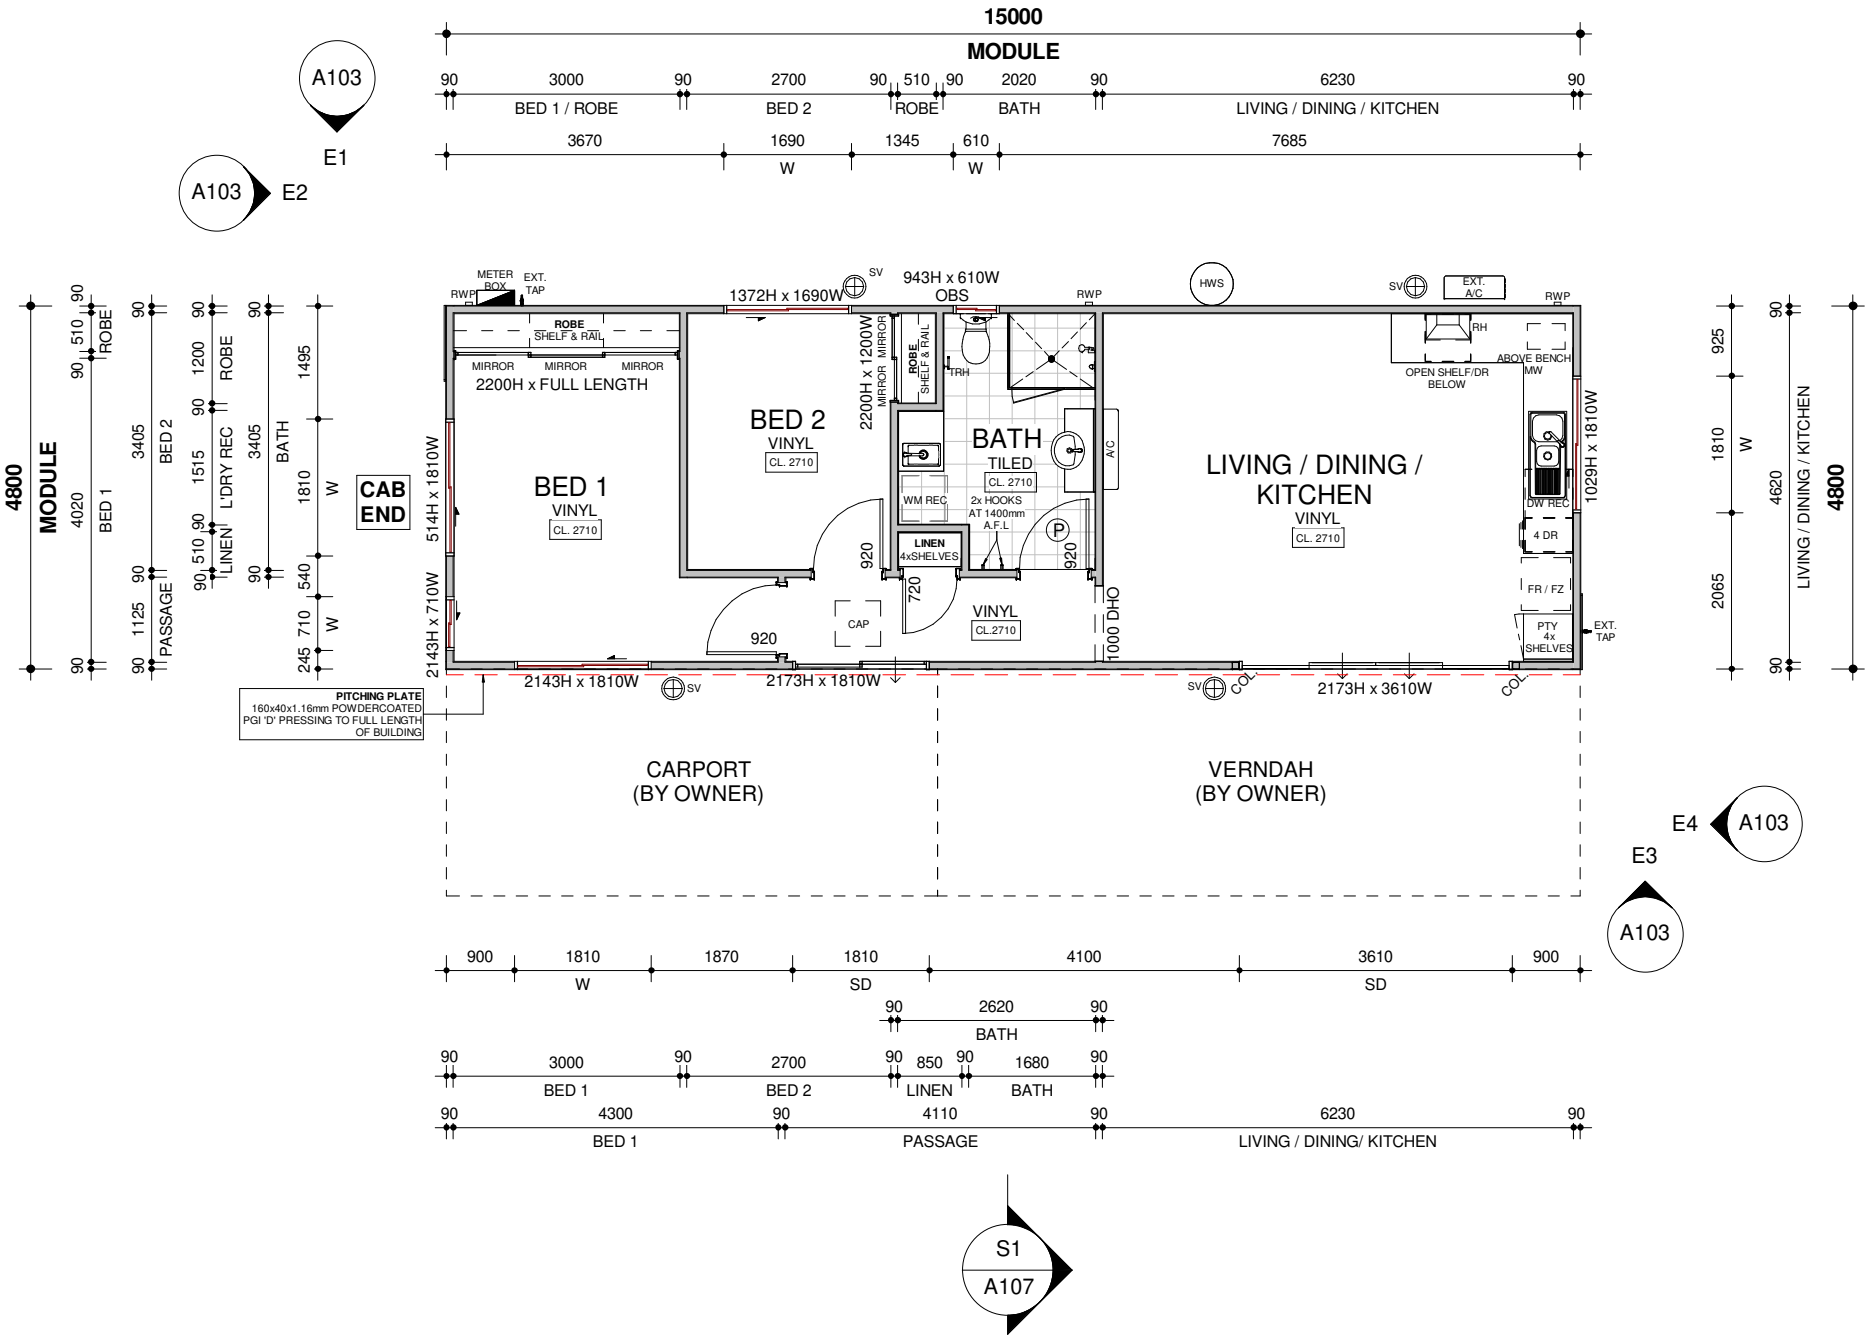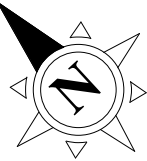

AREA	
BUILDING	72.00m²
VERANDAH	N/A
CARPORT	N/A
PERGOLA	N/A
TOTAL	72.00m²

ROOF AREA	
ROOF (YARD BUILT)	70.19m²
ROOF (SITE BUILT)	N/A
TOTAL	70.19m²

1 FLOOR PLAN
A102 1 : 100

CLIENT: PROPERTY FRIENDS PTY LTD

ADDRESS: LOT 91 BROWNLIE STREET,
WAGGRAKINE WA 6530

HOUSE TYPE: INDICATIVE - 2x1 DWELLING


Rev	Description	Date
F	Add 4th carbay on site plan	20/02/26
G	Update final plans as per CV-1	19/03/26
H	Updated sliding door height for B2 & concrete slab plan for set-down	19/03/26
I	Relocate MW to above bench, MW recess to become open shelf, add DGPO/USB to kitchen, update DGPO/Isolator in kitchen	15/04/26
J	Add pitching plate to full length of building	28/04/26
K	Update site information	29/04/26

JOB No.	25278
DATE:	29/04/2026 3:15:04 PM
DRAWN:	BT
CHECKED:	WI
REV:	SHEET
SCALE:	1 : 100




T: 08 64540919 F: 08 64540918
W: modularwa.com.au
e: sales@modularwa.com.au
Builders reg # 101630


Use figured dimensions in preference to scaled.
All dimensions to be verified and checked on the job. © .

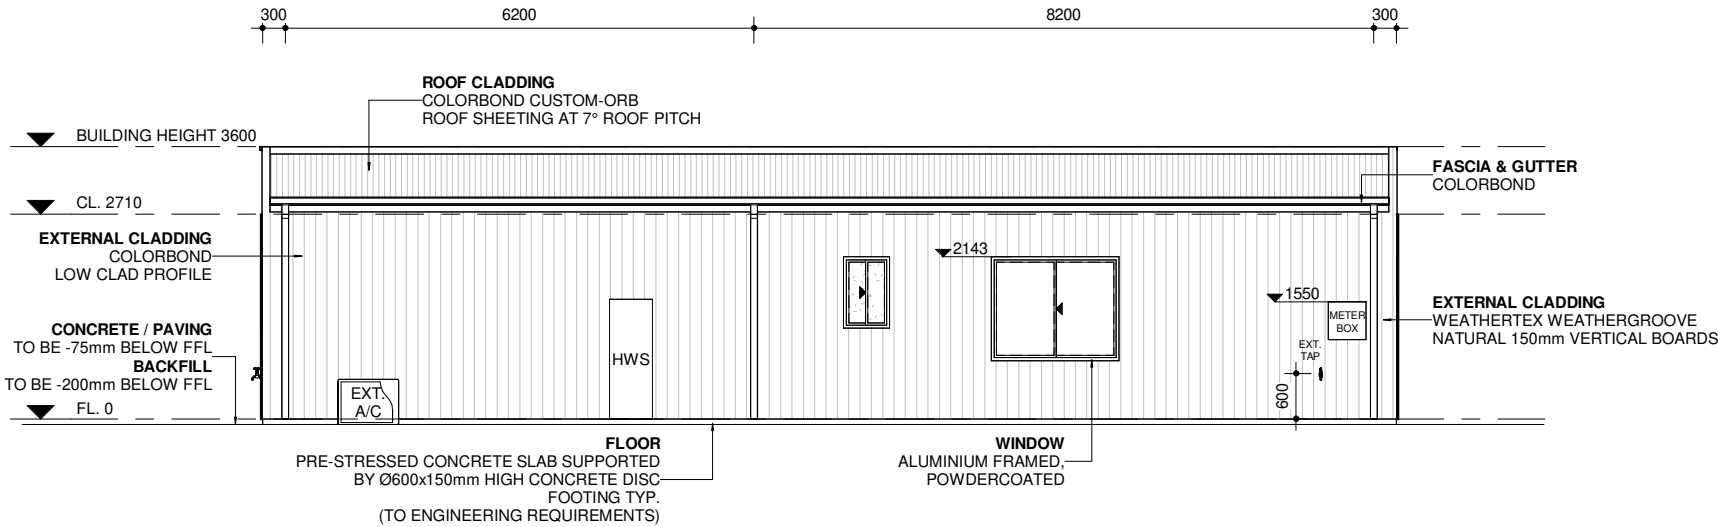


E1 E1 ELEVATION
A103 1 : 100

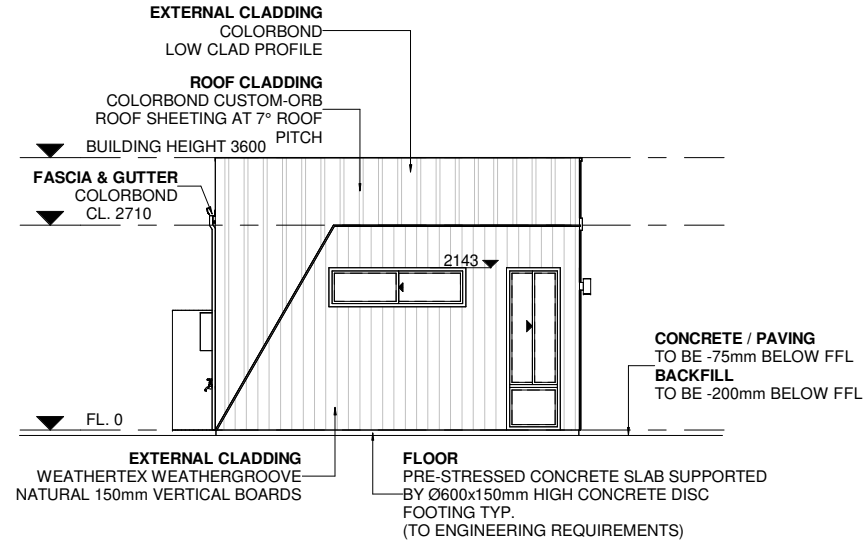

E2 E2 ELEVATION
A103 1 : 100

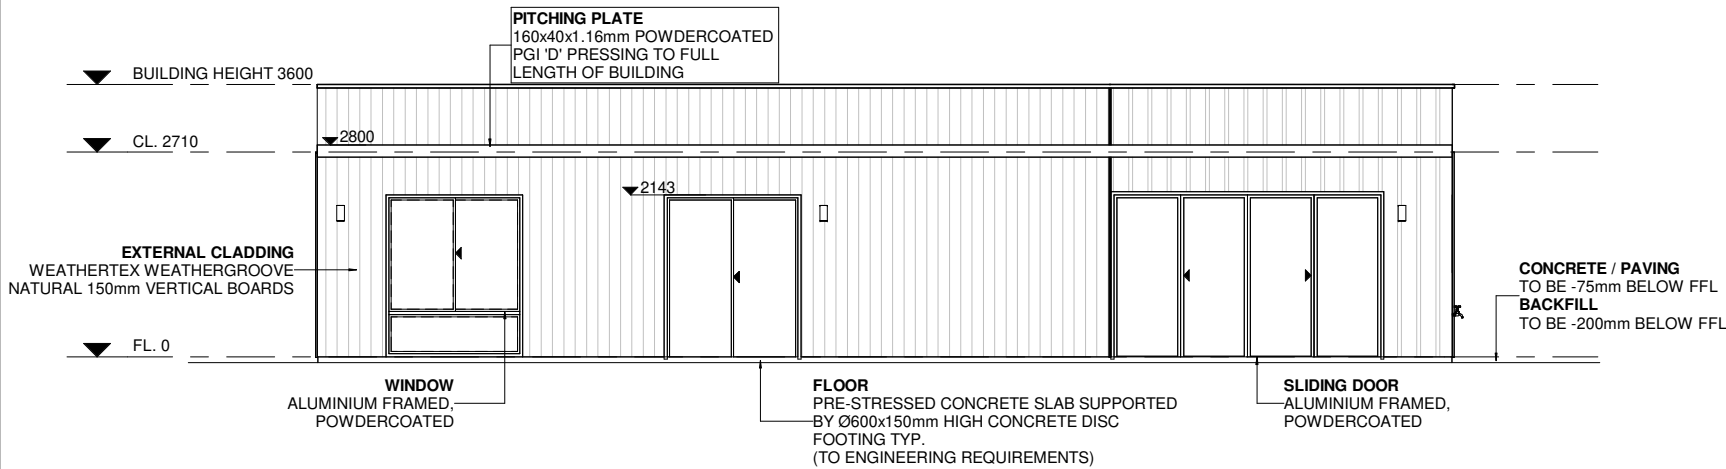

E3 E3 ELEVATION
A103 1 : 100

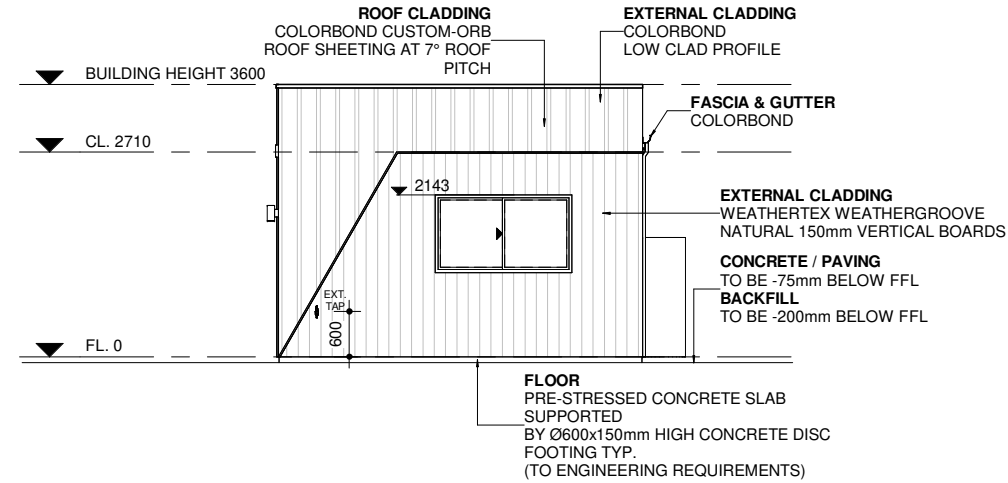

E4 E4 ELEVATION
A103 1 : 100

CLIENT:	PROPERTY FRIENDS PTY LTD	<table><tr><th>Rev</th><th>Description</th><th>Date</th></tr><tr><td>F</td><td>Add 4th carbay on site plan</td><td>20/02/26</td></tr><tr><td>G</td><td>Update final plans as per CV-1</td><td>19/03/26</td></tr><tr><td>H</td><td>Updated sliding door height for B2 & concrete slab plan for set-down</td><td>19/03/26</td></tr><tr><td>I</td><td>Relocate MW to above bench, MW recess to become open shelf, add DGPO/USB to kitchen, update DGPO/Isolator in kitchen</td><td>15/04/26</td></tr><tr><td>J</td><td>Add pitching plate to full length of building</td><td>28/04/26</td></tr><tr><td>K</td><td>Update site information</td><td>29/04/26</td></tr></table>	Rev	Description	Date	F	Add 4th carbay on site plan	20/02/26	G	Update final plans as per CV-1	19/03/26	H	Updated sliding door height for B2 & concrete slab plan for set-down	19/03/26	I	Relocate MW to above bench, MW recess to become open shelf, add DGPO/USB to kitchen, update DGPO/Isolator in kitchen	15/04/26	J	Add pitching plate to full length of building	28/04/26	K	Update site information	29/04/26
Rev	Description		Date																				
F	Add 4th carbay on site plan		20/02/26																				
G	Update final plans as per CV-1		19/03/26																				
H	Updated sliding door height for B2 & concrete slab plan for set-down		19/03/26																				
I	Relocate MW to above bench, MW recess to become open shelf, add DGPO/USB to kitchen, update DGPO/Isolator in kitchen		15/04/26																				
J	Add pitching plate to full length of building	28/04/26																					
K	Update site information	29/04/26																					
ADDRESS:	LOT 91 BROWNLIE STREET, WAGGRAKINE WA 6530																						
HOUSE TYPE:	INDICATIVE - 2x1 DWELLING																						

JOB No.	25278	 T: 08 64540919 F: 08 64540918 W: modularwa.com.au e: sales@modularwa.com.au Builders reg # 101630 Use figured dimensions in preference to scaled. All dimensions to be verified and checked on the job. © .
DATE:	29/04/2026 3:15:05 PM	
DRAWN:	BT	
CHECKED:	WI	
REV:	SHEET	
SCALE:	K 1 : 100	
A103		


ELECTRICAL LEGEND	
	CEILING LIGHT - L.E.D OYSTER FITTING
	CEILING LIGHT - L.E.D DOWNLIGHT FITTING
	CEILING LIGHT - L.E.D PENDANT FITTING
	EXTERNAL WALL LIGHT
	EXTERNAL WALL LIGHT - UP/DOWN
	EXTERNAL FLOOD LIGHT - WITH SENSOR
	L.E.D. SURFACE MOUNTED BATTEN
	MOTION SENSOR
	SINGLE GPO
	DOUBLE GPO
	DOUBLE GPO c/w USB OUTLET
	QUAD GPO
	SINGLE WEATHERPROOF GPO
	DOUBLE WEATHERPROOF GPO
	ISOLATION SWITCH
	ISOLATION SWITCH c/w SGPO ON SINGLE SWITCH PLATE
	AIR CONDITIONER UNIT ISOLATOR
	PHONE / DATA OUTLET
	TV POINT
	LIGHT SWITCH
	CLIPSAL FIRETEK 755PSMA4 HARDWIRED SMOKE DETECTOR c/w BATTERY BACKUP AS SHOWN
	EXHAUST FAN FLUMED
	HEAT / LIGHT / FAN
	VENTAIR AIRBUS 250mm ROUND WHITE WITH L.E.D EXHAUST FAN/LIGHT COMBO AS SHOWN
	METER BOX
	GAS NEGUS - NOT APPLICABLE TO THIS PROJECT

ELECTRICAL NOTES:

1. ALL ELECTRICAL HEIGHTS ARE MEASURED FROM FINISHED FLOOR LEVEL.
2. ALL LIGHT SWITCHES TO BE 1200mm ABOVE FINISHED FLOOR LEVEL UNLESS OTHERWISE NOTED.
3. INTERNAL GENERAL POWER OUTLETS, PHONE & DATA POINTS TO BE 300mm ABOVE FINISHED FLOOR LEVEL UNLESS OTHERWISE NOTED.
4. EXTERNAL GENERAL POWER OUTLETS AND EXTERNAL ISO SWITCH TO BE 1200mm ABOVE FINISHED FLOOR LEVEL UNLESS OTHERWISE NOTED.
5. EXTERNAL LIGHT FITTINGS TO BE 1900mm ABOVE FINISHED FLOOR LEVEL - MEASURED TO UNDERSIDE OF FITTING.
6. POWER TO DISHWASHER RECESS, ELECTRIC OVEN, RANGEHOOD, HOT PLATE, HOT WATER SYSTEM.
7. ISOLATOR SWITCH TO BE ABOVE WATER INLET/OUTLET PIPE OF HOUSE AT 1200mm ABOVE FINISHED FLOOR LEVEL.

AIR CONDITIONING NOTE:

1. ALL EXTERNAL A/C BOOTS TO BE LOCATED MIN. 400mm ABOVE FFL.

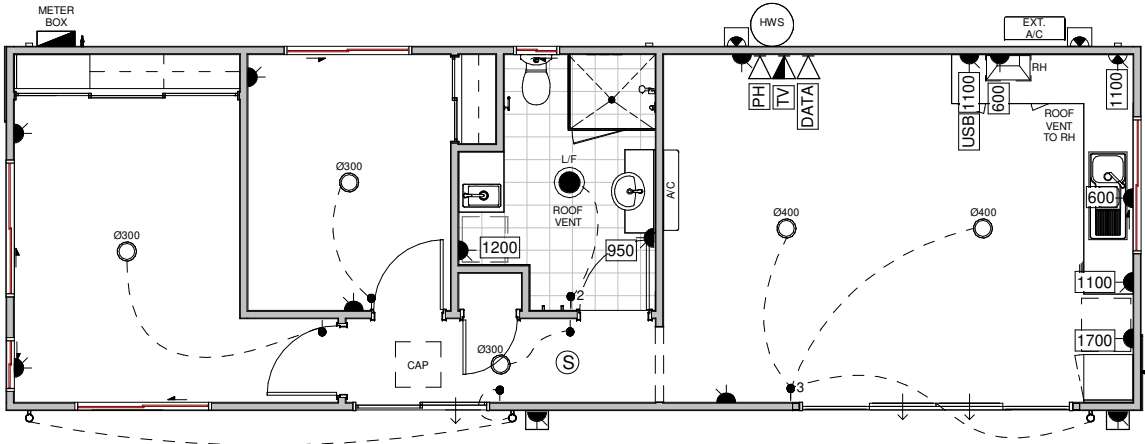

1

A104

ELECTRICAL PLAN

1 : 100

CLIENT:	PROPERTY FRIENDS PTY LTD
ADDRESS:	LOT 91 BROWNLIE STREET, WAGGRAKINE WA 6530
HOUSE TYPE:	INDICATIVE - 2x1 DWELLING

Rev	Description	Date
F	Add 4th carbay on site plan	20/02/26
G	Update final plans as per CV-1	19/03/26
H	Updated sliding door height for B2 & concrete slab plan for set-down	19/03/26
I	Relocate MW to above bench, MW recess to become open shelf, add DGPO/USB to kitchen, update DGPO/Isolator in kitchen	15/04/26
J	Add pitching plate to full length of building	28/04/26
K	Update site information	29/04/26

JOB No.	25278
DATE:	29/04/2026 3:15:05 PM
DRAWN:	BT
CHECKED:	WI
REV:	SHEET
SCALE:	1 : 100




T: 08 64540919 F: 08 64540918
W: modularwa.com.au
e: sales@modularwa.com.au
Builders reg # 101630

Use figured dimensions in preference to scaled.
All dimensions to be verified and checked on the job. © .


NOTE:
OWNER TO SUPPLY & INSTALL
PORTABLE HOT PLATE

NO HANDLES TO DRAWERS, CUPBOARDS & OHC.
REFER TO CUPBOARD FINGER GRIP DETAIL 'FG'


NOTE:
DIMENSIONS SHOWN ARE
FROM INTERNAL WALL LINING

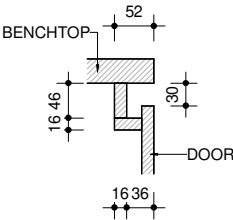


FG CUPBOARD FINGER GRIP DETAIL
A105 1 : 10

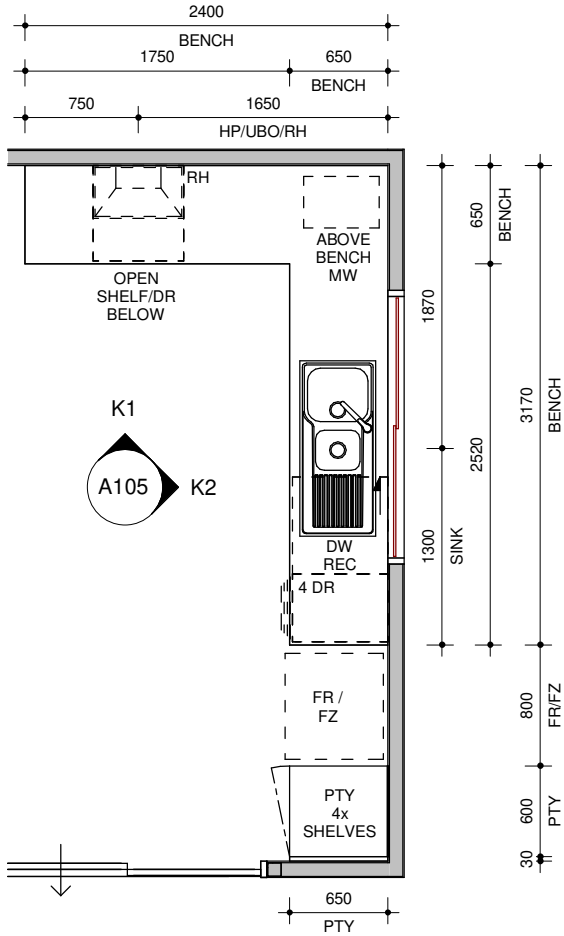

K KITCHEN LAYOUT
A105 1 : 50

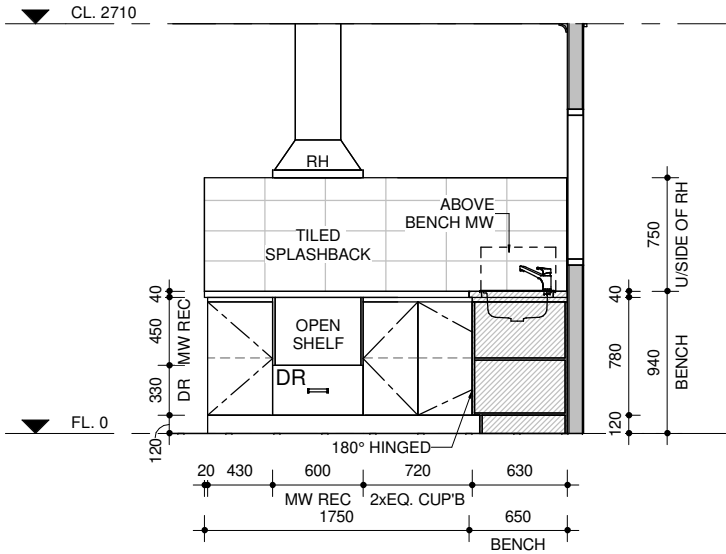

K1 K1 KITCHEN
A105 1 : 50

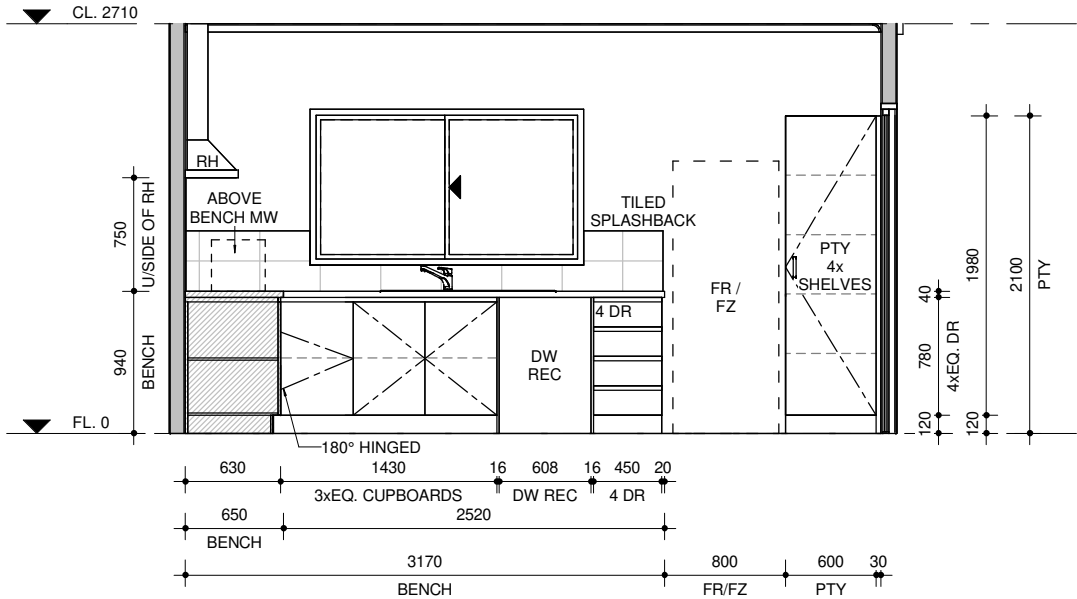


K2 K2 KITCHEN
A105 1 : 50


CLIENT:	PROPERTY FRIENDS PTY LTD	<table><tr><th>Rev</th><th>Description</th><th>Date</th></tr><tr><td>F</td><td>Add 4th carbay on site plan</td><td>20/02/26</td></tr><tr><td>G</td><td>Update final plans as per CV-1</td><td>19/03/26</td></tr><tr><td>H</td><td>Updated sliding door height for B2 & concrete slab plan for set-down</td><td>19/03/26</td></tr><tr><td>I</td><td>Relocate MW to above bench, MW recess to become open shelf, add DGPO/USB to kitchen, update DGPO/Isolator in kitchen</td><td>15/04/26</td></tr><tr><td>J</td><td>Add pitching plate to full length of building</td><td>28/04/26</td></tr><tr><td>K</td><td>Update site information</td><td>29/04/26</td></tr></table>	Rev	Description	Date	F	Add 4th carbay on site plan	20/02/26	G	Update final plans as per CV-1	19/03/26	H	Updated sliding door height for B2 & concrete slab plan for set-down	19/03/26	I	Relocate MW to above bench, MW recess to become open shelf, add DGPO/USB to kitchen, update DGPO/Isolator in kitchen	15/04/26	J	Add pitching plate to full length of building	28/04/26	K	Update site information	29/04/26	JOB No.	25278	 T: 08 64540919 F: 08 64540918 W: modularwa.com.au e: sales@modularwa.com.au Builders reg # 101630 Use figured dimensions in preference to scaled. All dimensions to be verified and checked on the job. © .
Rev	Description		Date																							
F	Add 4th carbay on site plan		20/02/26																							
G	Update final plans as per CV-1		19/03/26																							
H	Updated sliding door height for B2 & concrete slab plan for set-down		19/03/26																							
I	Relocate MW to above bench, MW recess to become open shelf, add DGPO/USB to kitchen, update DGPO/Isolator in kitchen		15/04/26																							
J	Add pitching plate to full length of building	28/04/26																								
K	Update site information	29/04/26																								
ADDRESS:	LOT 91 BROWNLIE STREET, WAGGRAKINE WA 6530	DATE:	29/04/2026 3:15:06 PM																							
HOUSE TYPE:	INDICATIVE - 2x1 DWELLING	DRAWN:	BT																							
		CHECKED:	WI																							
		REV:	SHEET																							
		SCALE:	K																							
		As indicated		A105																						

NO HANDLES TO DRAWERS, CUPBOARDS & OHC.
REFER TO DWG. A105 FOR CUPBOARD
FINGER GRIP DETAIL 'FG'


NOTE:
DIMENSIONS SHOWN ARE
FROM INTERNAL WALL LINING

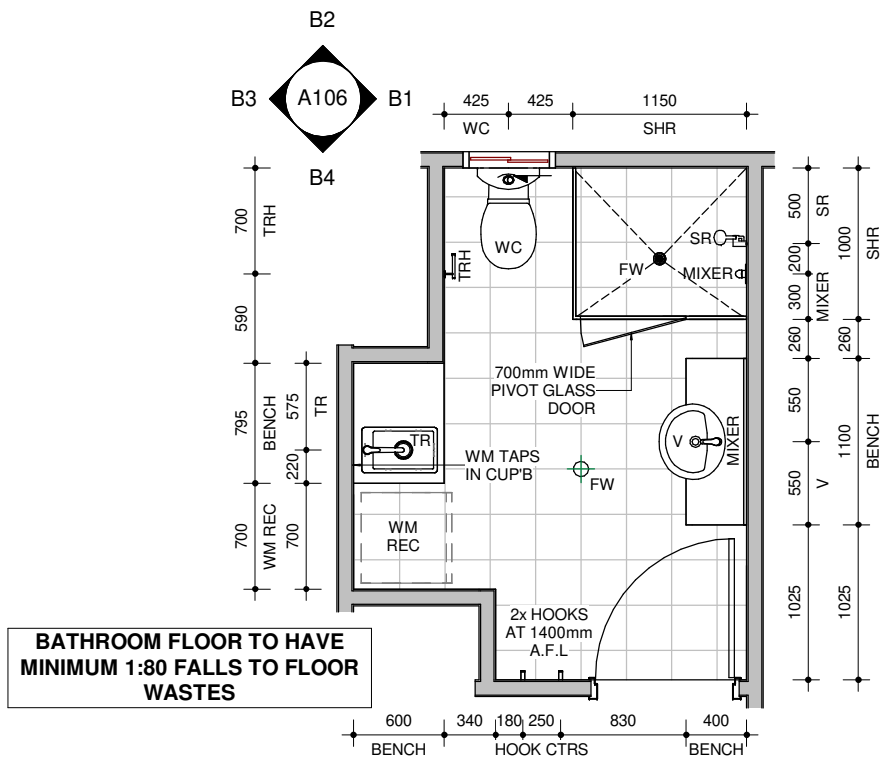


B BATH LAYOUT
A106 1 : 50

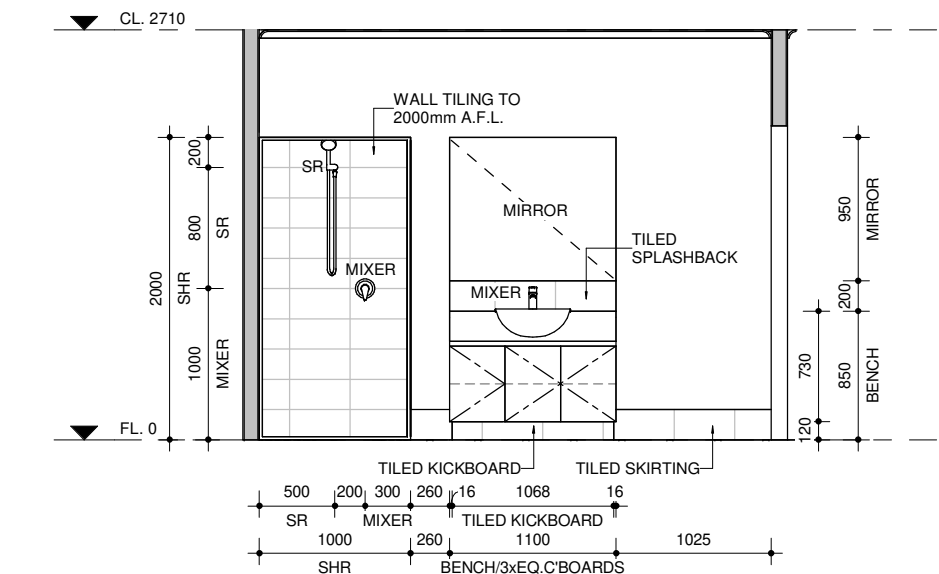


B1 B1 BATH
A106 1 : 50

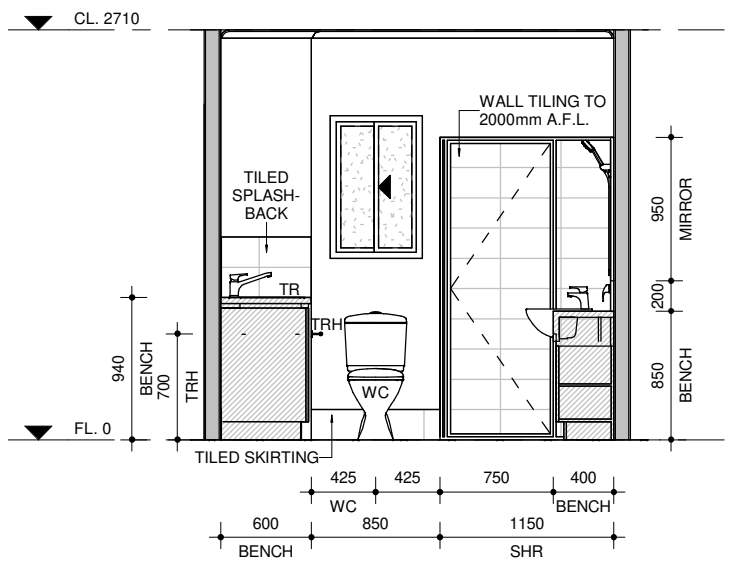

B2 B2 BATH
A106 1 : 50

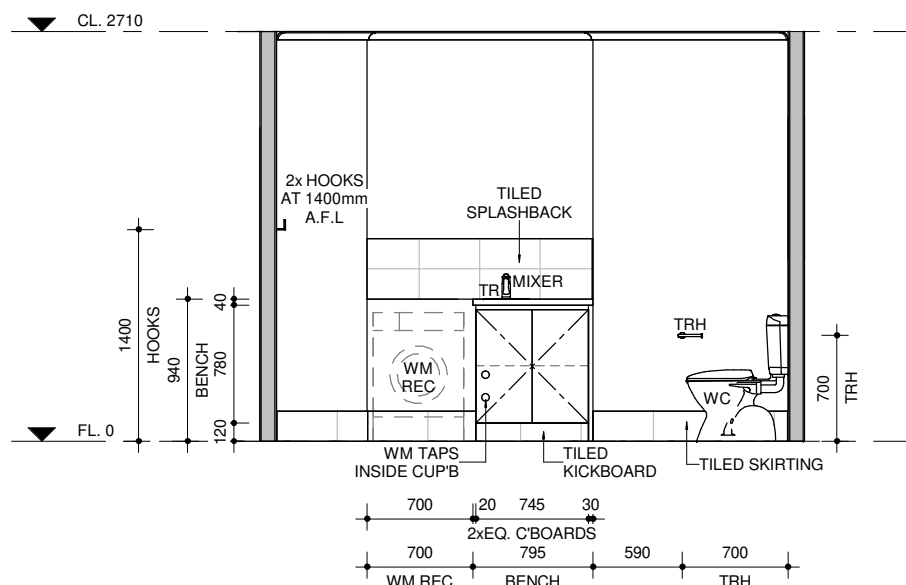

B3 B3 BATH
A106 1 : 50

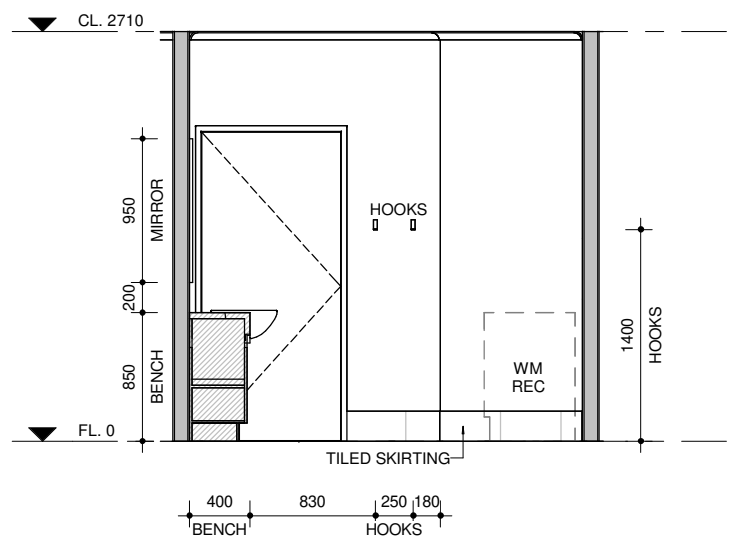

B4 B4 BATH
A106 1 : 50

CLIENT: PROPERTY FRIENDS PTY LTD

ADDRESS: LOT 91 BROWNLIE STREET,
WAGGRAKINE WA 6530

HOUSE TYPE: INDICATIVE - 2x1 DWELLING

Rev	Description	Date
F	Add 4th carbay on site plan	20/02/26
G	Update final plans as per CV-1	19/03/26
H	Updated sliding door height for B2 & concrete slab plan for set-down	19/03/26
I	Relocate MW to above bench, MW recess to become open shelf, add DGPO/USB to kitchen, update DGPO/Isolator in kitchen	15/04/26
J	Add pitching plate to full length of building	28/04/26
K	Update site information	29/04/26

JOB No. 25278

DATE: 29/04/2026 3:15:06 PM

DRAWN: BT

CHECKED: WI


REV: K

SCALE: 1 : 50


modularwa

T: 08 64540919 F: 08 64540918
W: modularwa.com.au
e: sales@modularwa.com.au
Builders reg # 101630


Use figured dimensions in preference to scaled.
All dimensions to be verified and checked on the job. © .

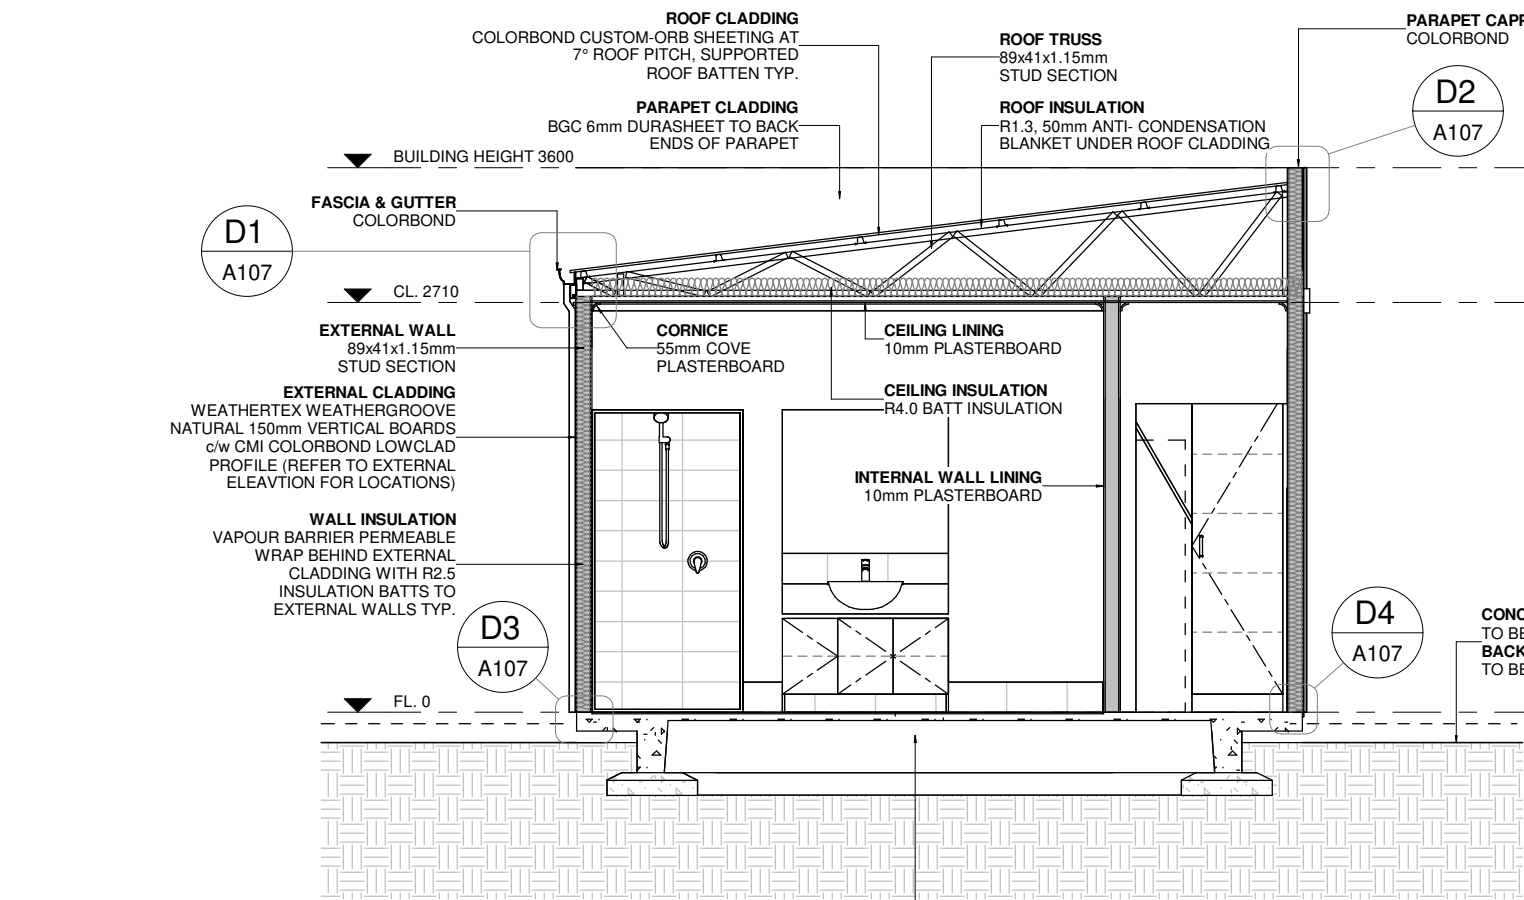


S1 BUILDING SECTION
A107 1 : 50

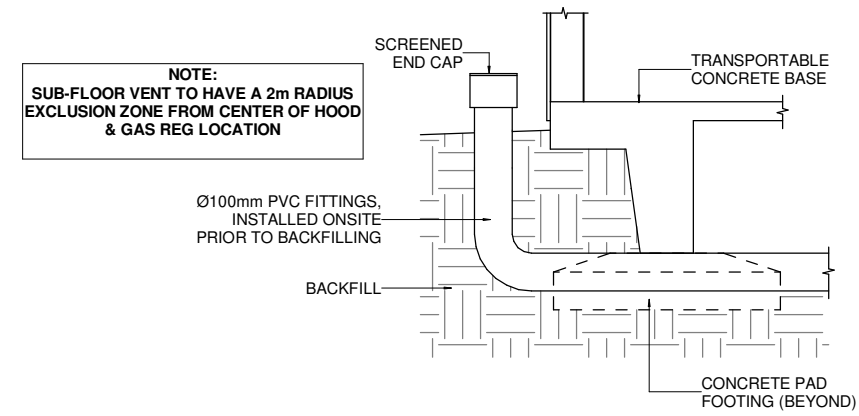


SV SUB FLOOR VENTILATION
A107 1 : 20

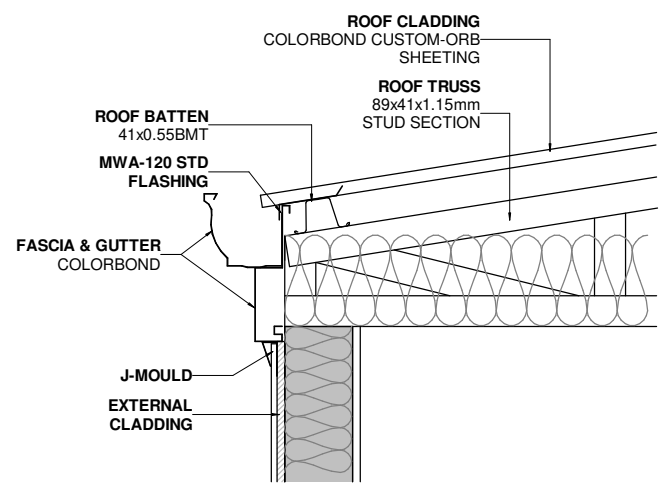


D1 GUTTER DETAIL
A107 1 : 10

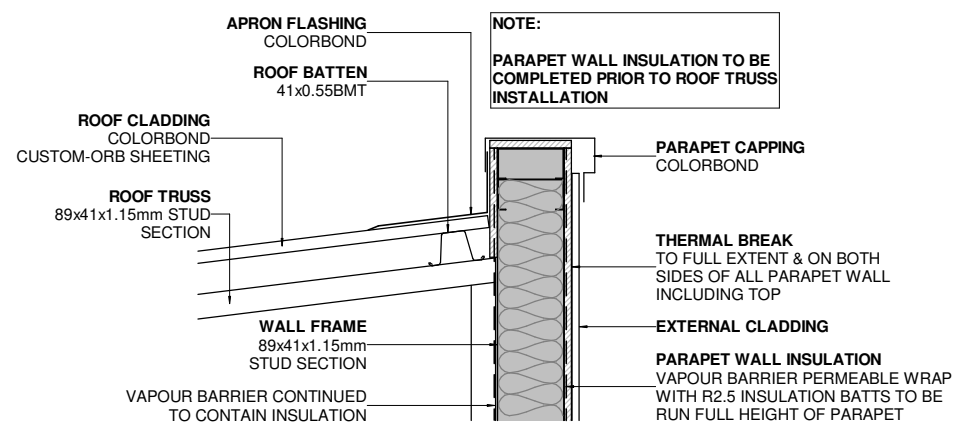

D2 PARAPET DETAIL
A107 1 : 10

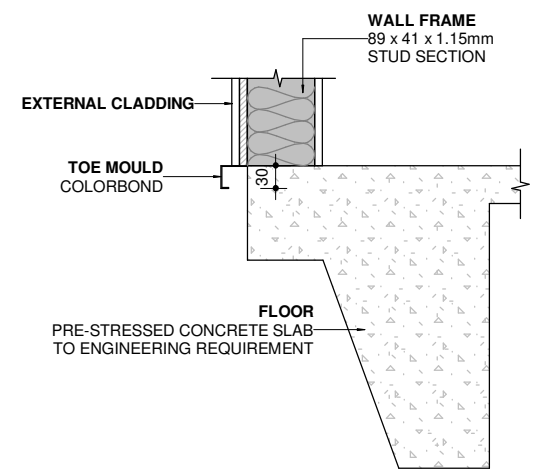

D3 TOE MOULD DETAIL
A107 1 : 10

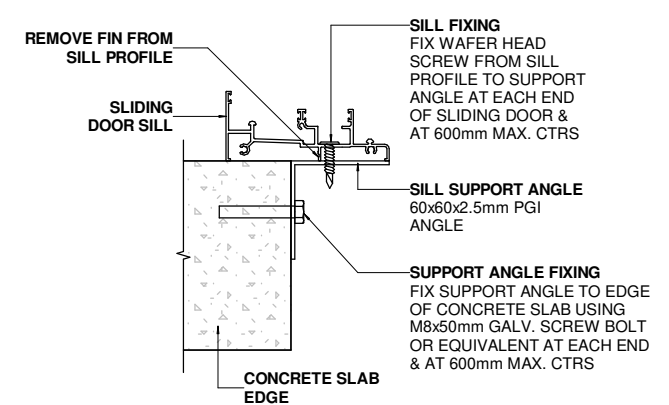

D4 SLIDING DOOR SILL SUPPORT DETAIL
A107 1 : 5


CLIENT:	PROPERTY FRIENDS PTY LTD	<table><tr><th>Rev</th><th>Description</th><th>Date</th></tr><tr><td>F</td><td>Add 4th carbay on site plan</td><td>20/02/26</td></tr><tr><td>G</td><td>Update final plans as per CV-1</td><td>19/03/26</td></tr><tr><td>H</td><td>Updated sliding door height for B2 & concrete slab plan for set-down</td><td>19/03/26</td></tr><tr><td>I</td><td>Relocate MW to above bench, MW recess to become open shelf, add DGPO/USB to kitchen, update DGPO/Isolator in kitchen</td><td>15/04/26</td></tr><tr><td>J</td><td>Add pitching plate to full length of building</td><td>28/04/26</td></tr><tr><td>K</td><td>Update site information</td><td>29/04/26</td></tr></table>	Rev	Description	Date	F	Add 4th carbay on site plan	20/02/26	G	Update final plans as per CV-1	19/03/26	H	Updated sliding door height for B2 & concrete slab plan for set-down	19/03/26	I	Relocate MW to above bench, MW recess to become open shelf, add DGPO/USB to kitchen, update DGPO/Isolator in kitchen	15/04/26	J	Add pitching plate to full length of building	28/04/26	K	Update site information	29/04/26	JOB No.	25278	 T: 08 64540919 F: 08 64540918 W: modularwa.com.au e: sales@modularwa.com.au Builders reg # 101630 Use figured dimensions in preference to scaled. All dimensions to be verified and checked on the job. © .
Rev	Description		Date																							
F	Add 4th carbay on site plan		20/02/26																							
G	Update final plans as per CV-1		19/03/26																							
H	Updated sliding door height for B2 & concrete slab plan for set-down		19/03/26																							
I	Relocate MW to above bench, MW recess to become open shelf, add DGPO/USB to kitchen, update DGPO/Isolator in kitchen		15/04/26																							
J	Add pitching plate to full length of building	28/04/26																								
K	Update site information	29/04/26																								
ADDRESS:	LOT 91 BROWNLIE STREET, WAGGRAKINE WA 6530	DATE:	29/04/2026 3:15:07 PM																							
HOUSE TYPE:	INDICATIVE - 2x1 DWELLING	DRAWN:	BT																							
		CHECKED:	WI																							
		REV:	SHEET																							
		SCALE:	K As A107																							

FOUNDATION NOTES:

1. FOUNDATION SOIL TO BE CLEAN, COMPACT, NATURAL GROUND, FREE OF EXCESSIVE MOISTURE.
2. GROUND SHALL BE COMPACTED TO ACHIEVE: FOR SAND SITES, MINIMUM 6 BLOWS OVER 150-450 MM, 7 BLOWS OVER 450-750 MM, AND 9 BLOWS OVER 750-1050 MM WITH A PERTH SAND PENETROMETER (AS1289.6.3.3) FOR COHESIVE/GRAVEL SITES, MINIMUM 6 BLOWS OVER 150MM USING A DYNAMIC CONE PENETROMETER (DCP) THROUGH ALL FILL OR TO 600MM IN NATURAL GROUND.
3. PREPARE SITE SUCH THAT SURFACE RUNOFF CANNOT DRAIN OVER OR UNDER FOUNDATIONS.
4. FOOTING HAS BEEN DESIGNED FOR SOIL CLASS "TBC"

DO NOT SCALE FROM THIS DRAWING
ALL CONTRACTORS TO CHECK DIMENSIONS AND NOTES PRIOR TO COMMENCEMENT OF ANY WORKS AND ANY DISCREPANCIES TO BE NOTIFIED TO THE SITE SUPERVISOR WITHOUT DELAY.

PENETRATIONS		
CIP	CAST IN PLATE	150 SQ
FW	FLOOR WASTE	65Ø
VB	VANITY BASIN	65Ø
KS	KITCHEN SINK	65Ø
TR	TROUGH	65Ø
WC	WC PAN	125Ø
SHR	SHOWER WASTE	125Ø

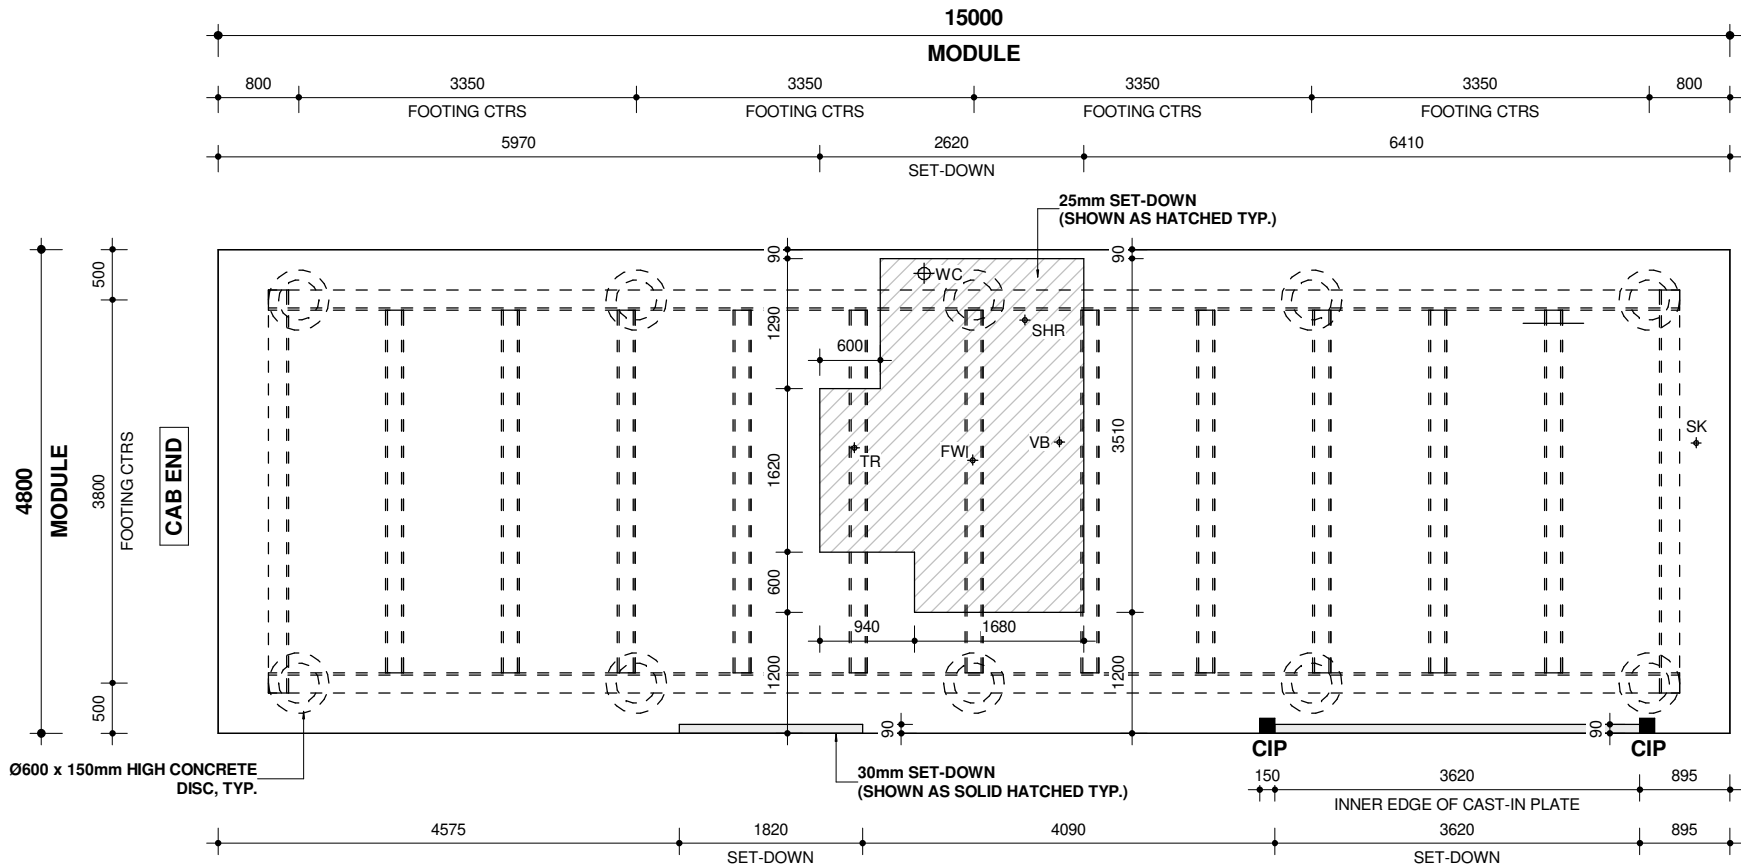

1

CONCRETE SLAB PLAN

A108

1 : 75

CLIENT:	PROPERTY FRIENDS PTY LTD	<table><tr><th>Rev</th><th>Description</th><th>Date</th></tr><tr><td>F</td><td>Add 4th carbay on site plan</td><td>20/02/26</td></tr><tr><td>G</td><td>Update final plans as per CV-1</td><td>19/03/26</td></tr><tr><td>H</td><td>Updated sliding door height for B2 & concrete slab plan for set-down</td><td>19/03/26</td></tr><tr><td>I</td><td>Relocate MW to above bench, MW recess to become open shelf, add DGPO/USB to kitchen, update DGPO/Isolator in kitchen</td><td>15/04/26</td></tr><tr><td>J</td><td>Add pitching plate to full length of building</td><td>28/04/26</td></tr><tr><td>K</td><td>Update site information</td><td>29/04/26</td></tr></table>	Rev	Description	Date	F	Add 4th carbay on site plan	20/02/26	G	Update final plans as per CV-1	19/03/26	H	Updated sliding door height for B2 & concrete slab plan for set-down	19/03/26	I	Relocate MW to above bench, MW recess to become open shelf, add DGPO/USB to kitchen, update DGPO/Isolator in kitchen	15/04/26	J	Add pitching plate to full length of building	28/04/26	K	Update site information	29/04/26	JOB No.	25278	 T: 08 64540919 F: 08 64540918 W: modularwa.com.au e: sales@modularwa.com.au Builders reg # 101630 Use figured dimensions in preference to scaled. All dimensions to be verified and checked on the job. © .
Rev	Description		Date																							
F	Add 4th carbay on site plan		20/02/26																							
G	Update final plans as per CV-1		19/03/26																							
H	Updated sliding door height for B2 & concrete slab plan for set-down		19/03/26																							
I	Relocate MW to above bench, MW recess to become open shelf, add DGPO/USB to kitchen, update DGPO/Isolator in kitchen		15/04/26																							
J	Add pitching plate to full length of building		28/04/26																							
K	Update site information	29/04/26																								
ADDRESS:	LOT 91 BROWNLIE STREET, WAGGRAKINE WA 6530	DATE:	29/04/2026 3:15:07 PM																							
HOUSE TYPE:	INDICATIVE - 2x1 DWELLING	DRAWN:	BT																							
		CHECKED:	WI																							
		REV:	SHEET																							
		SCALE:	K																							
		As indicated																								