



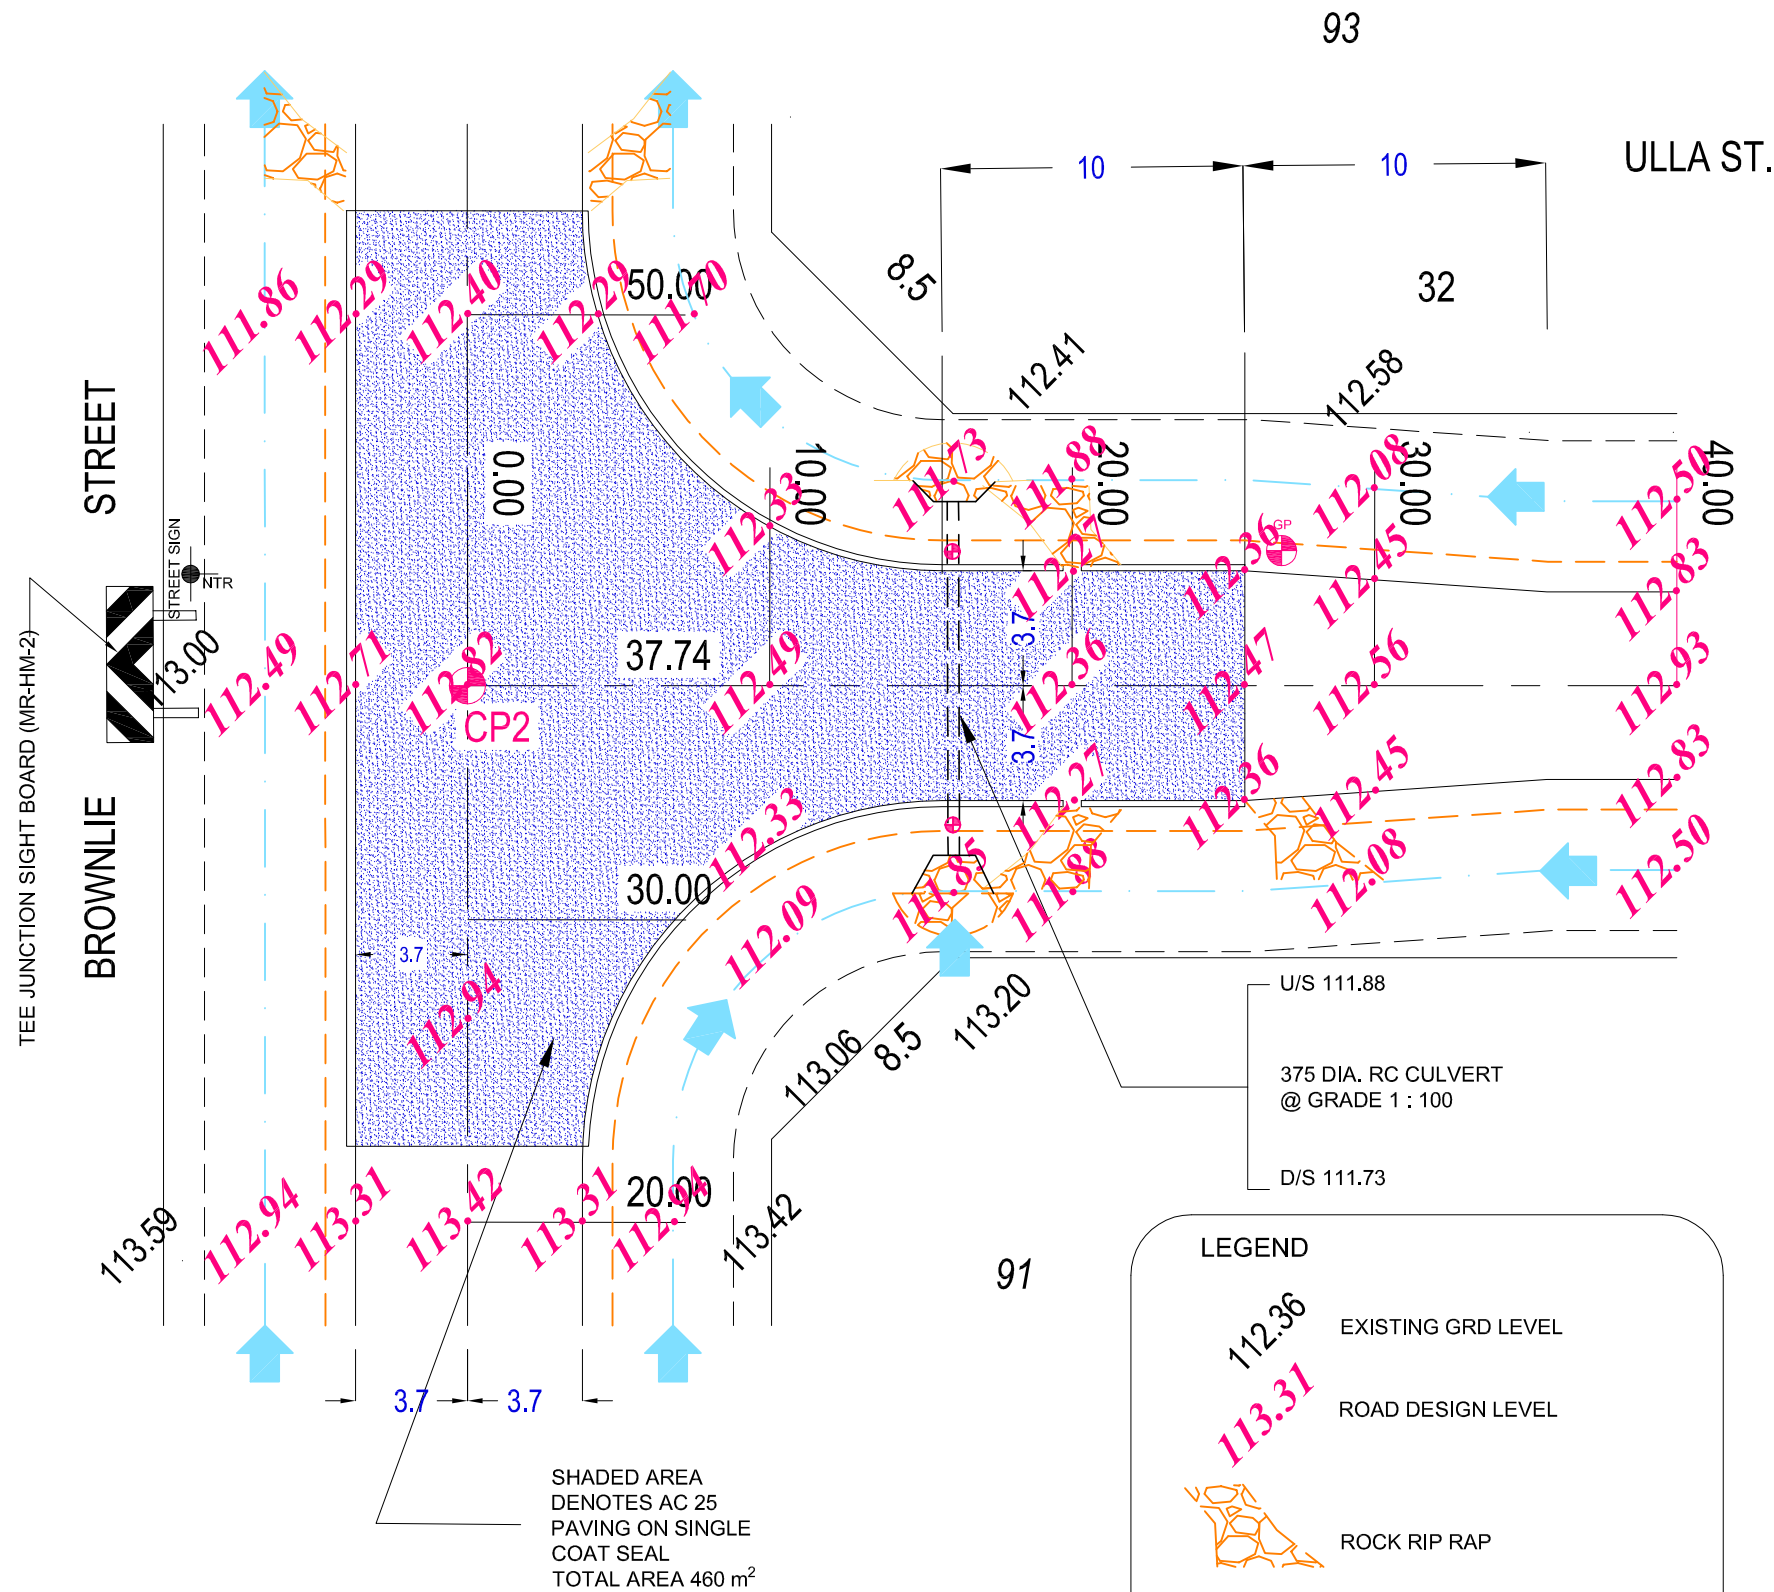

- LEGEND
- 112.36 EXISTING GRD LEVEL
- 113.31 ROAD DESIGN LEVEL
- ROCK RIP RAP
- DRAIN FLOW DIRECTION
- COMPACTED GRAVEL PAVING
- AC 25 PAVING

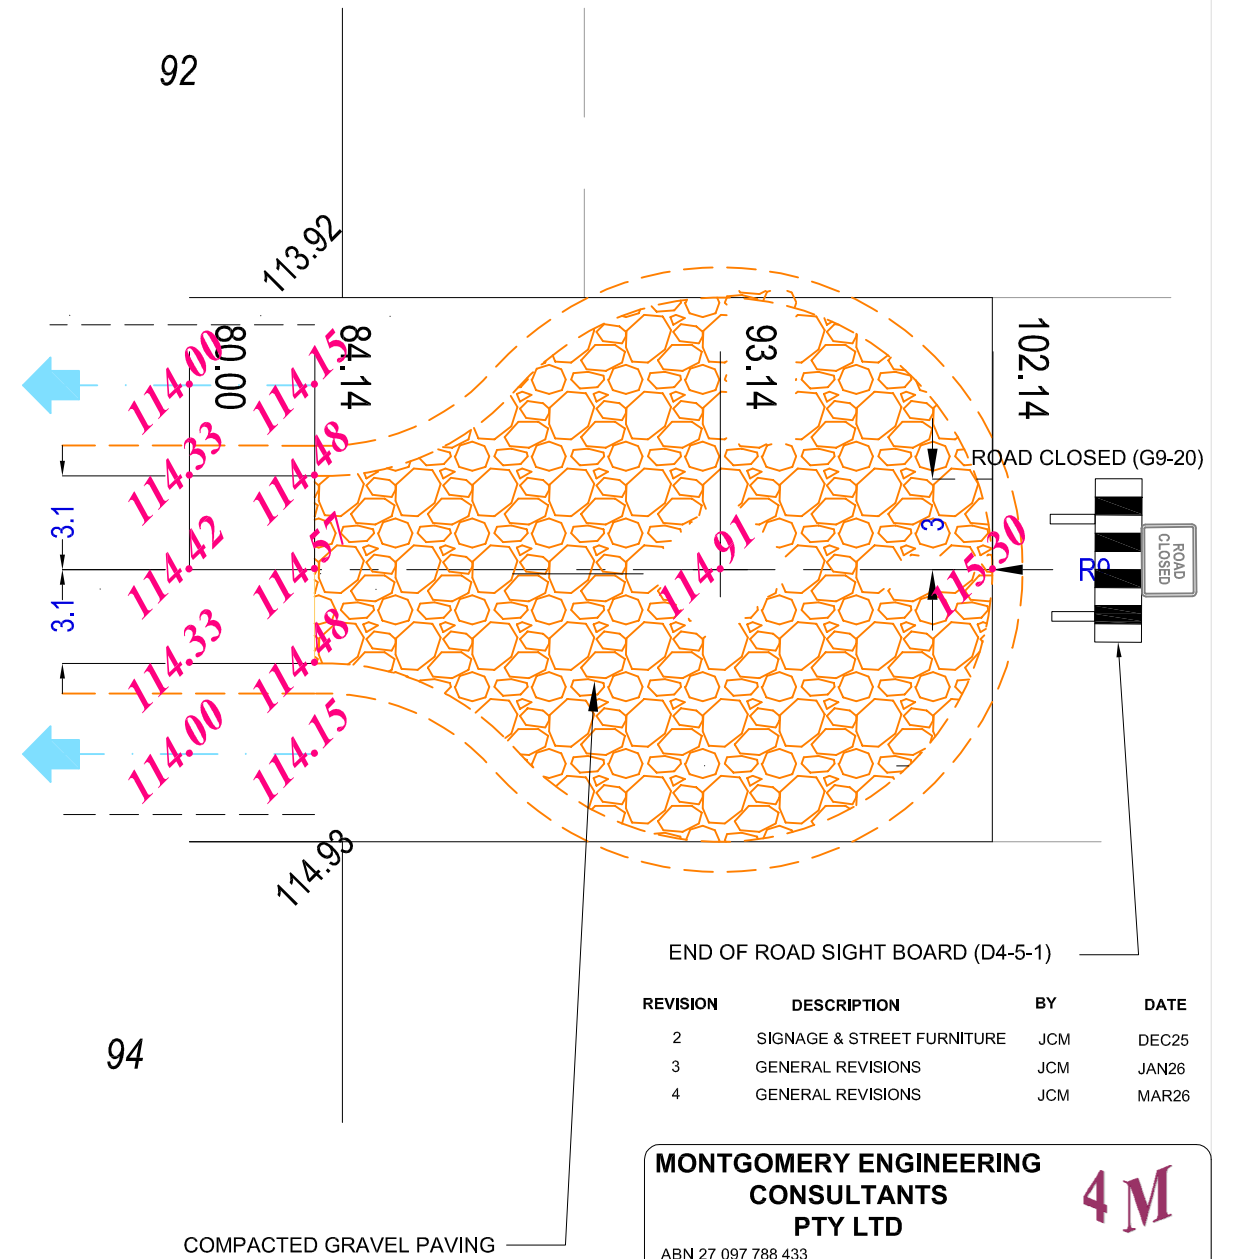

END OF ROAD SIGHT BOARD (D4-5-1)

REVISION	DESCRIPTION	BY	DATE
2	SIGNAGE & STREET FURNITURE	JCM	DEC25
3	GENERAL REVISIONS	JCM	JAN26
4	GENERAL REVISIONS	JCM	MAR26

MONTGOMERY ENGINEERING CONSULTANTS PTY LTD

4M

ABN 27 097 788 433
TEL: 9964 4640 FAX: 9964 4200 MOB: 0427 644 640
EMAIL: mecpl@wn.com.au

© 2001 THIS DRAWING REMAINS THE INTELLECTUAL PROPERTY OF MEC AND SHALL NOT BE ALTERED, COPIED OR USED FOR ANY OTHER PURPOSE THAN FOR THAT FOR WHICH IT IS ISSUED WITHOUT WRITTEN PERMISSION OF MEC.

WAVECREST ESTATES BROWNIE STREET - STAGE 1 INTERSECTION DETAIL			
SCALE:	1: 250 A3	DRAWN:	JCM
DATE:	SEP 25	DESIGNED:	JCM
BROWNIE ST - ULLA ST. INTERSECTION DETAIL			
C212460 - R - 050	REV:	4	REVIEWED:

