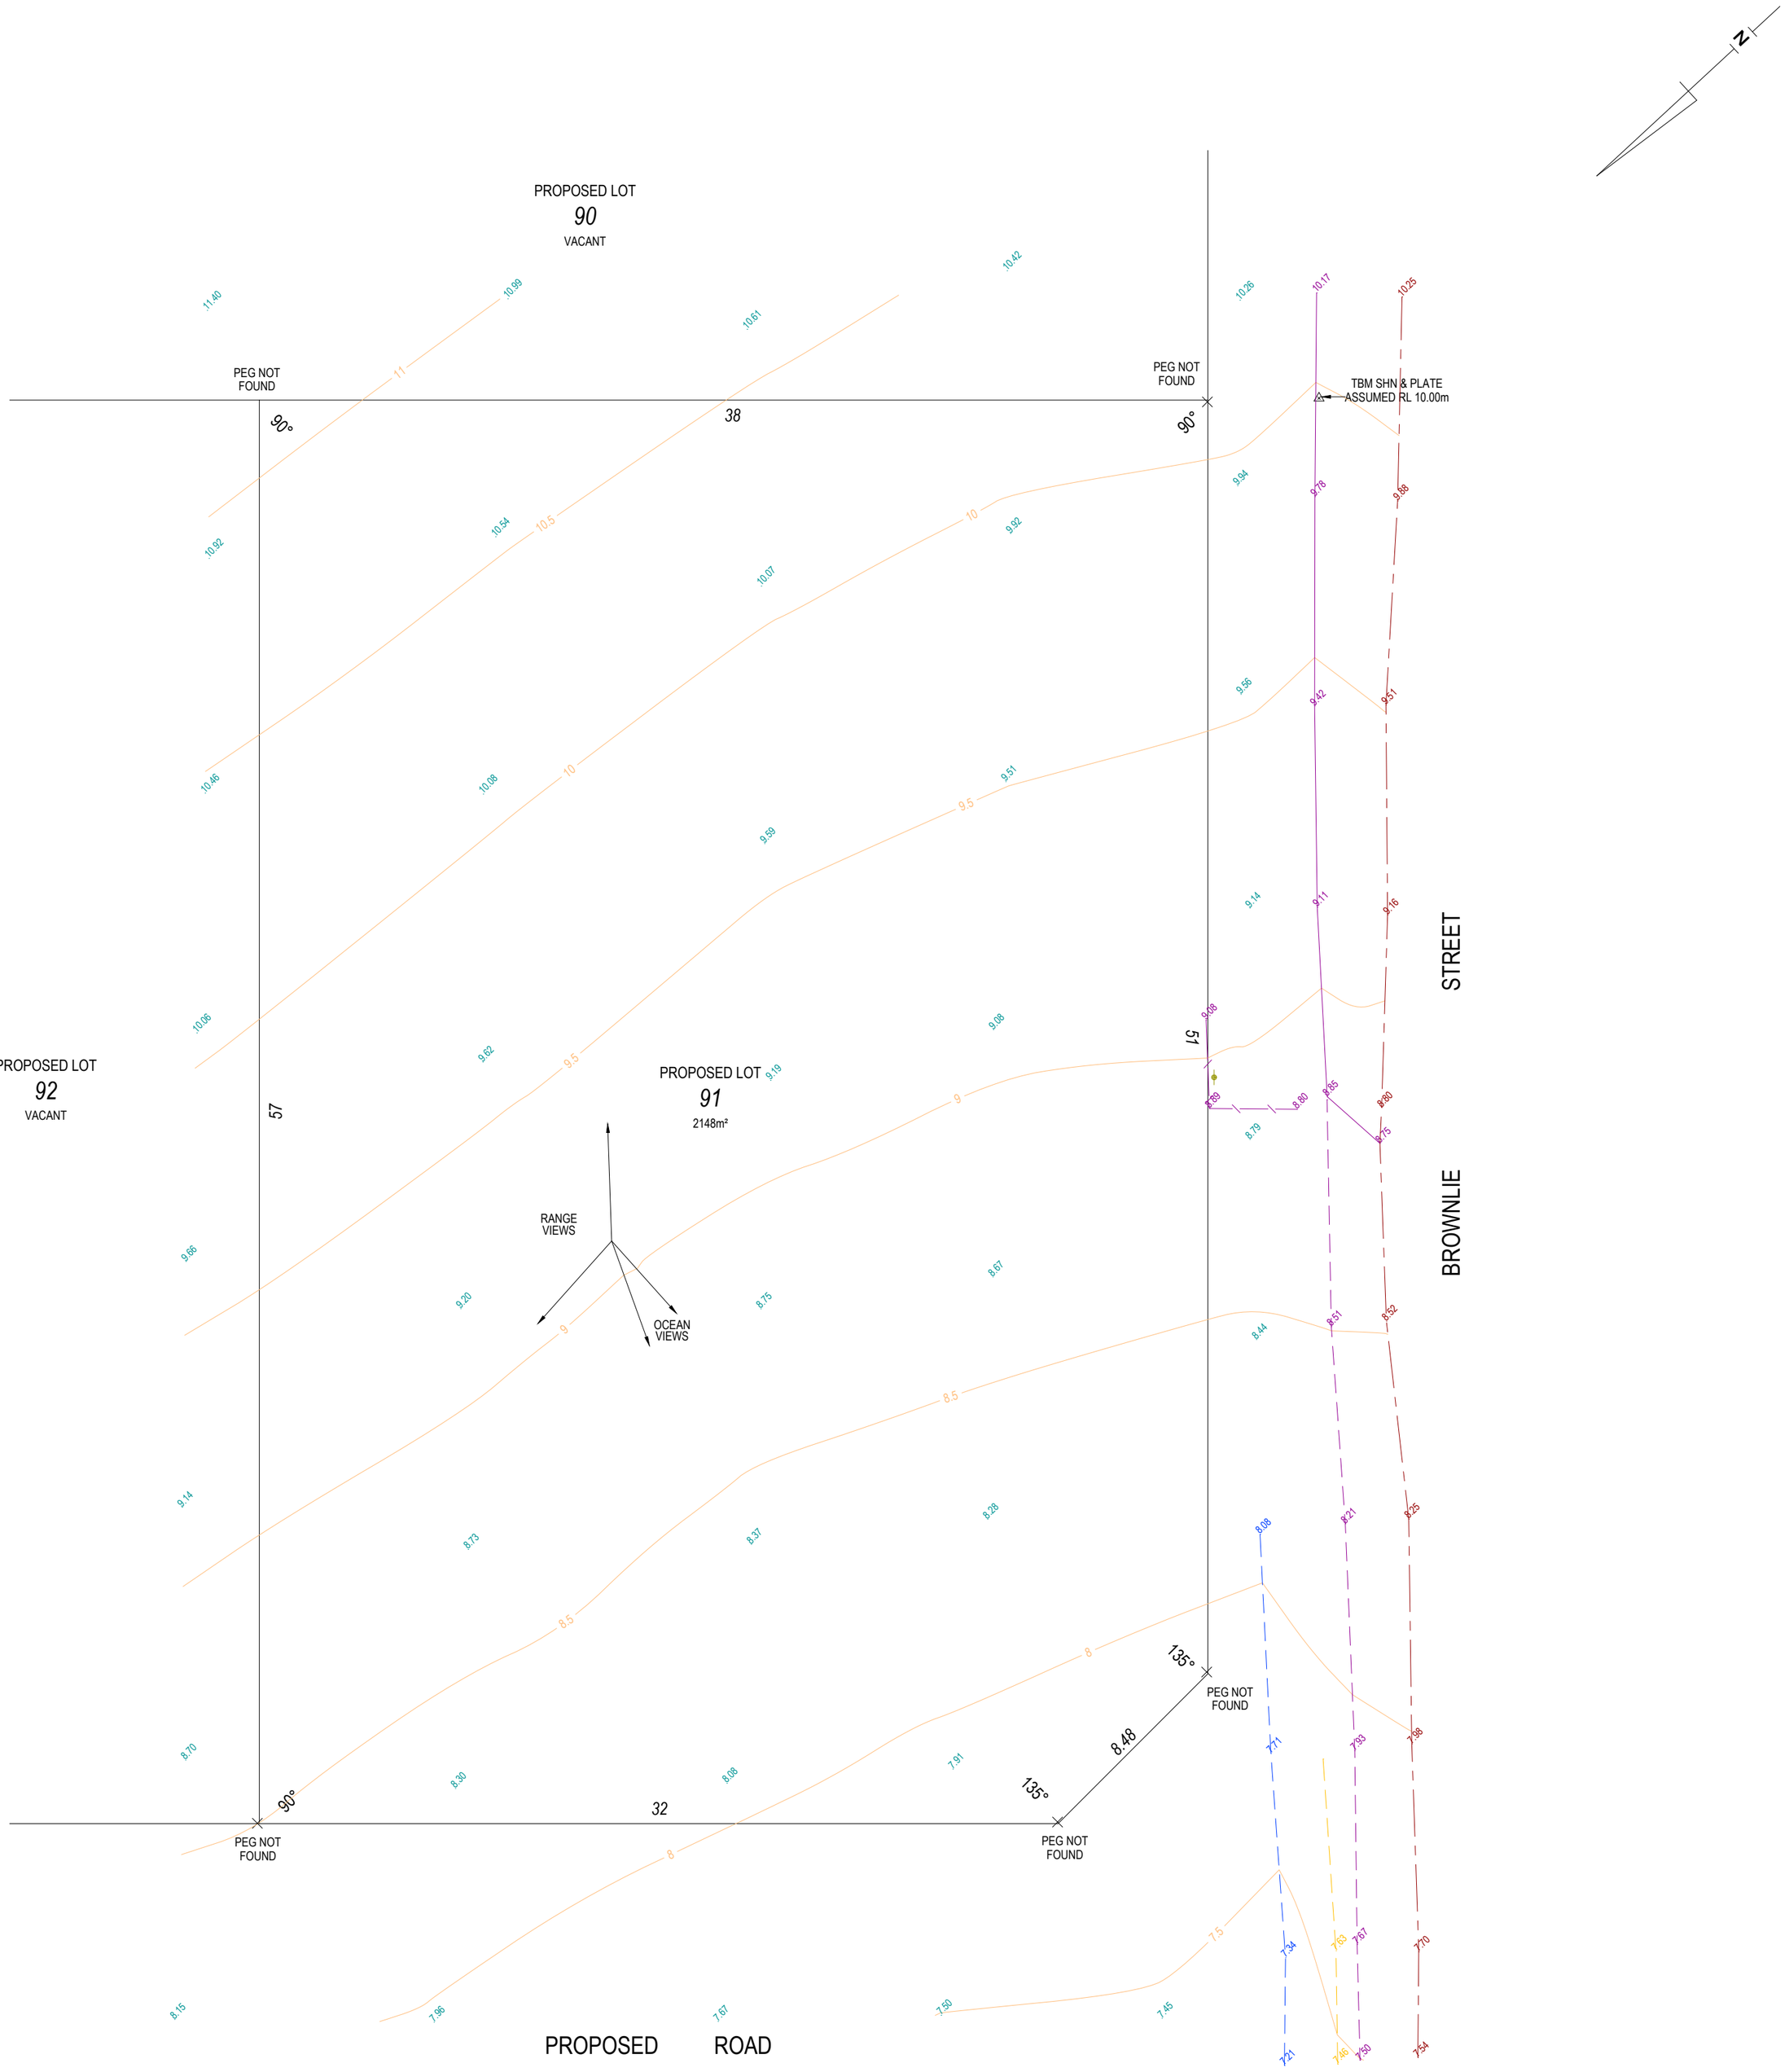


DISCLAIMER

THIS LOT IS ON A GREEN FIELD SITE THAT IS PROPOSED TO BE SUBDIVIDED. AS SUCH THERE ARE NO SURVEY PEGS, CONSTRUCTED ROAD OR CONSTRUCTED SERVICES TO THIS LOT. SEE LOT PRE-CALCULATION PLAN 25259PC01.PDF FOR DETAILS.

LEGEND

- T.B.M.
- SURVEY STAKE
- COMMUNICATIONS MARKER
- EDGE OF BITUMEN
- FENCE
- EDGE OF UNSEALED ROAD
- DRAIN
- ROAD SHOULDER
- CHANGE IN GRADE
- ROAD CENTRE

TITLE	: CONTOUR & FEATURE SURVEY
BUILDER	: -
CLIENT	: WBFREE PTY LTD
AUTHORITY	: CITY OF GREATER GERALDTON
LOCATION	: PROPOSED LOT 91 WAVECREST ESTATE, WAGGRAKINE

NOTES :

BOUNDARY & PEG POSITIONS NOT GUARANTEED
SURVEY LOCATES VISIBLE SERVICES ONLY - RING 'DIAL BEFORE YOU DIG' FOR UNDERGROUND SERVICE INFORMATION (1100)
POSITION OF UNDERGROUND SERVICES INTERPRETED FROM WATER CORPORATION SPATIAL DATABASE AND IS NOT GUARANTEED

SCALE : 1:200 @ A2

2 0 2 4 6 8 10 12

DEPOSITED PLAN : -

VOLUME/FOLIO : -

Quantum SURVEYS

P (08) 9965 0077
F (08) 9965 0088
PO Box 695
Geraldton WA 6531
info@quantumsurveys.com.au
quantumsurveys.com.au

SITE DETAILS :

Electrical	NO
Footpath	NO
Gas	NO
Kerb	NO
Road	BITUMEN / GRAVEL
Sewer	NO
Telecom	YES
Water	YES

DRAWN BY : D.WELSH

DATE : 16/01/2026

DATUM : ASSUMED

DRAWING No. :

25653- Lot 91